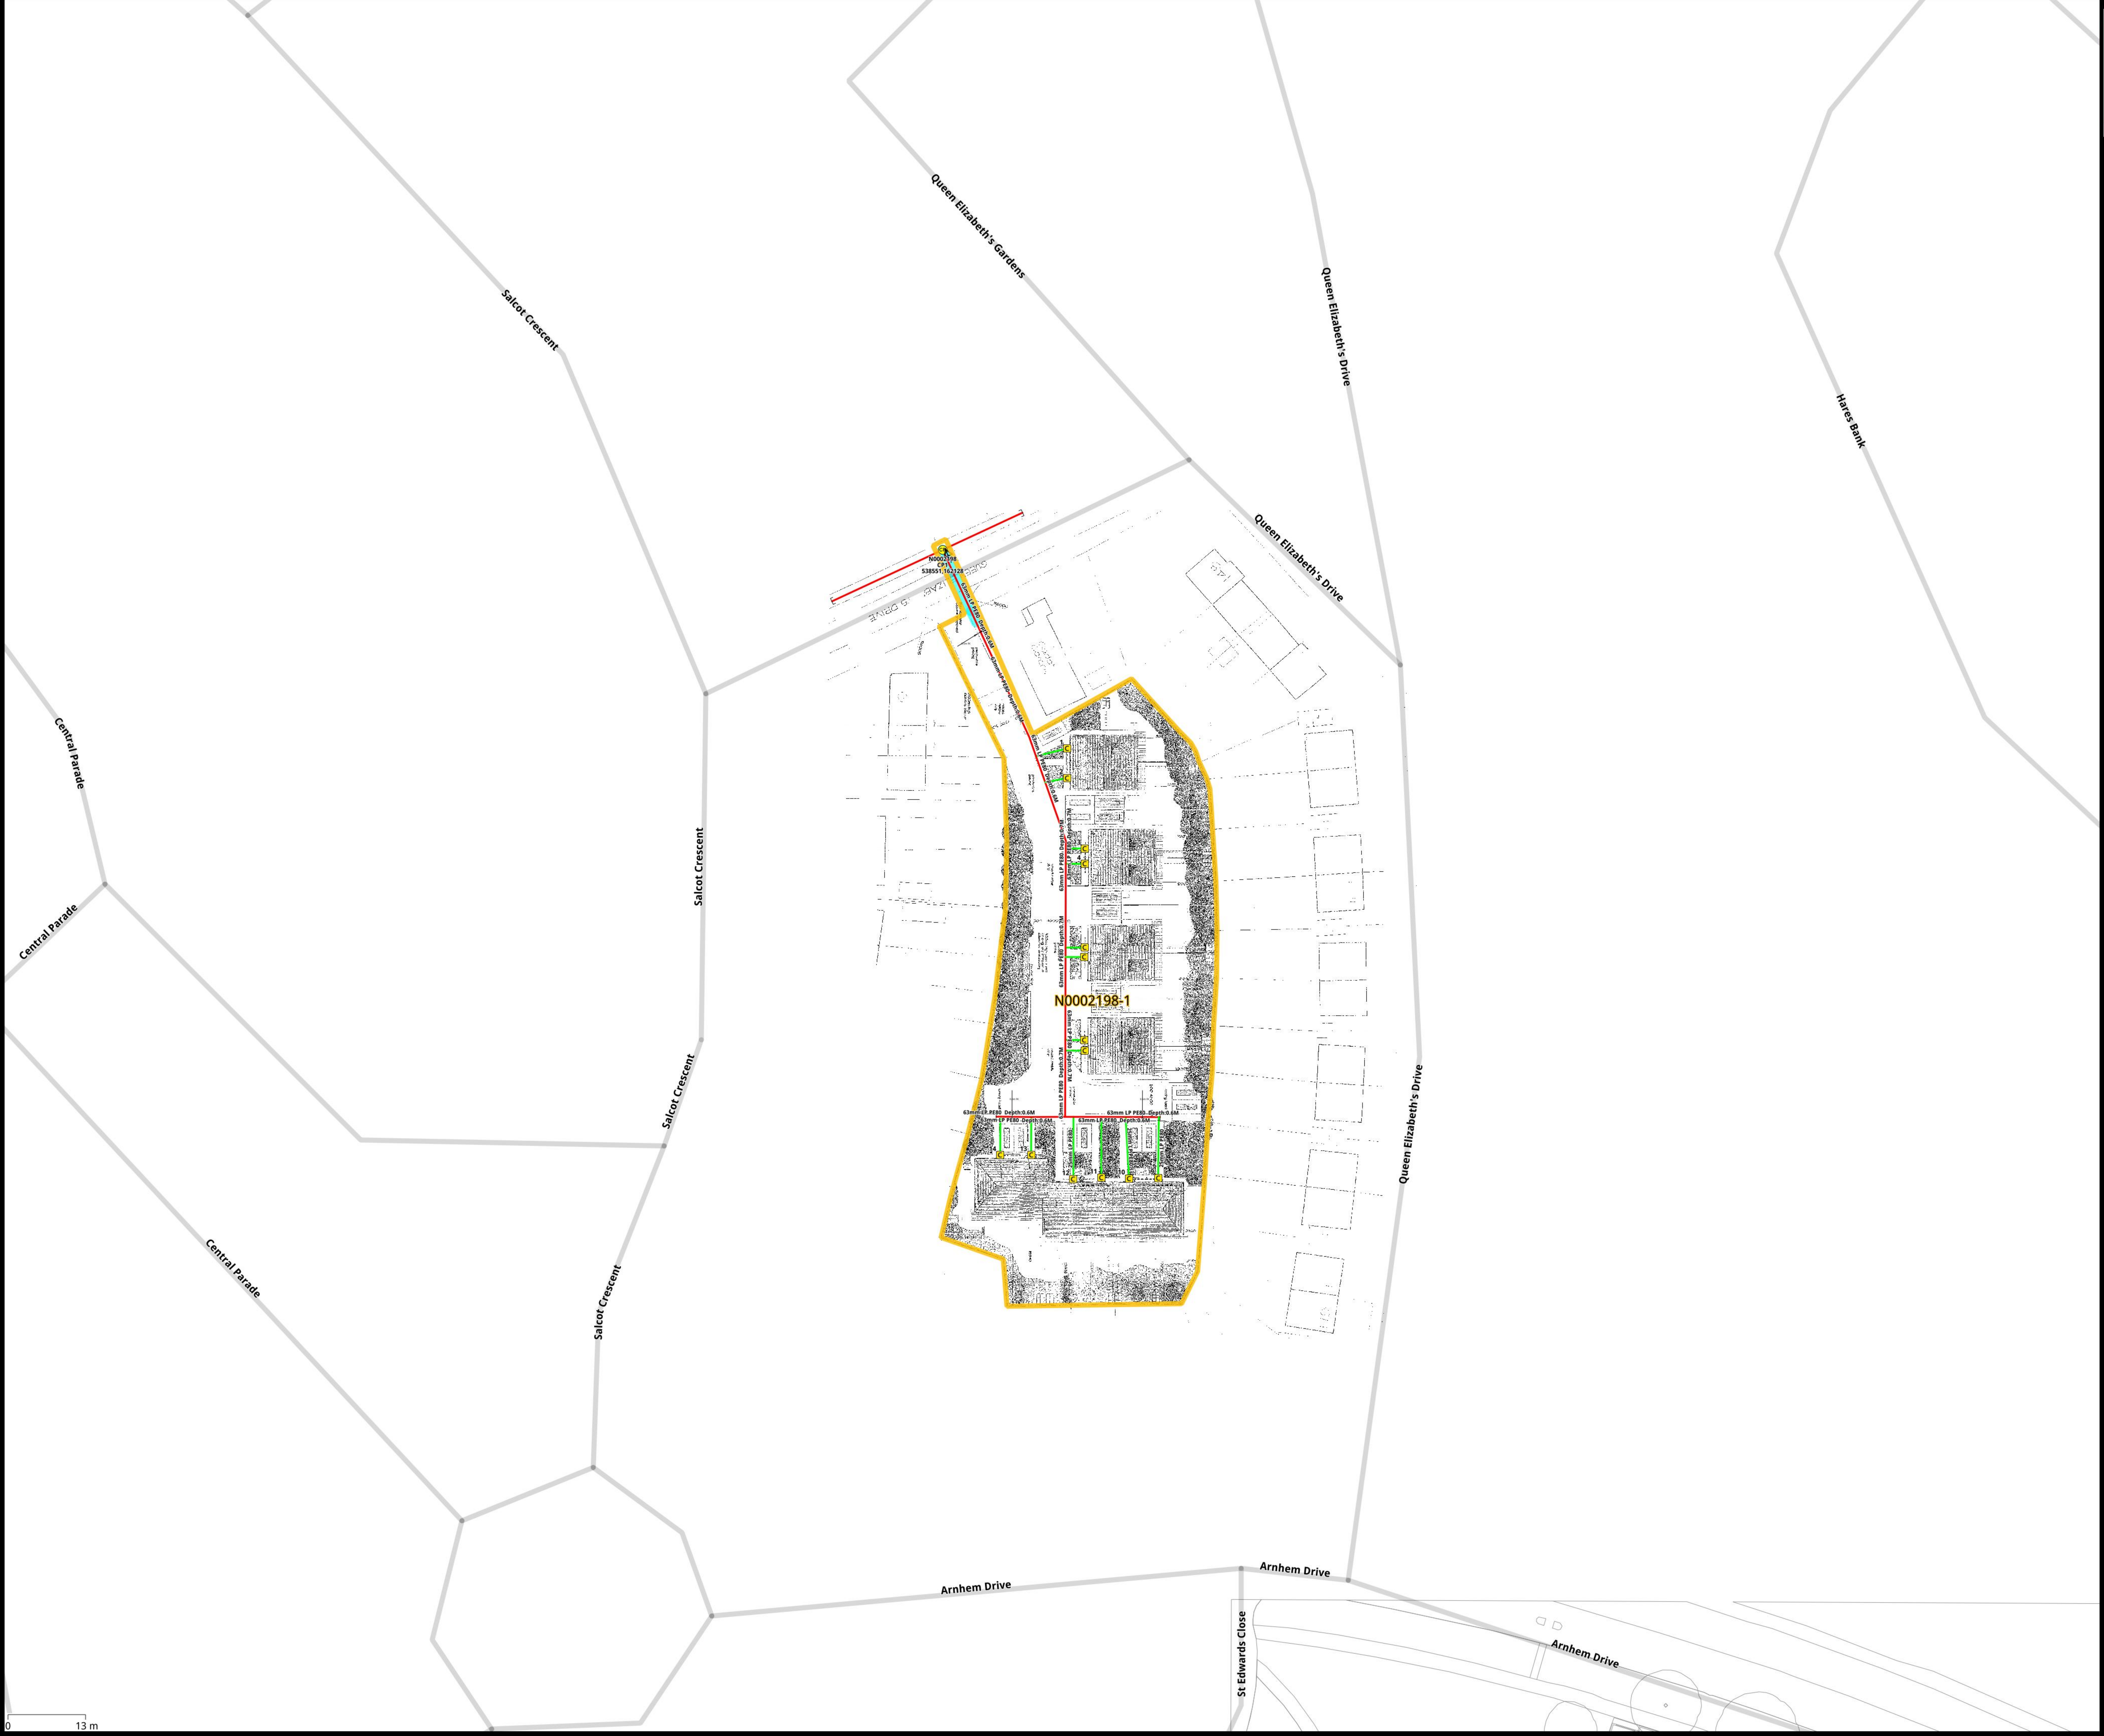
Salcot Crescent
Queen Elizabeth's Gardens
Queen Elizabeth's Drive
Hares Bank
Central Parade
Queen Elizabeth's Drive
Salcot Crescent
Central Parade
Salcot Crescent
Central Parade
Salcot Crescent
Queen Elizabeth's Drive
N0002198
CP1
538551, 162128
63mm LP PE80 Depth:0.6M
63mm LP PE80 Depth:0.6M
63mm LP PE80 Depth:0.6M
63mm LP PE80 Depth:0.7M
63mm LP PE80 Depth:0.7M
63mm LP PE80 Depth:0.7M
63mm LP PE80 Depth:0.7M
63mm LP PE80 Depth:0.7M
N0002198-1
63mm LP PE80 Depth:0.6M
63mm LP PE80 Depth:0.6M
63mm LP PE80 Depth:0.6M
63mm LP PE80 Depth:0.6M
25mm LP PE80
25mm LP PE80
3
4
14
13
12
11
10
Arnhem Drive
Arnhem Drive
Arnhem Drive
St Edwards Close
0
13 m

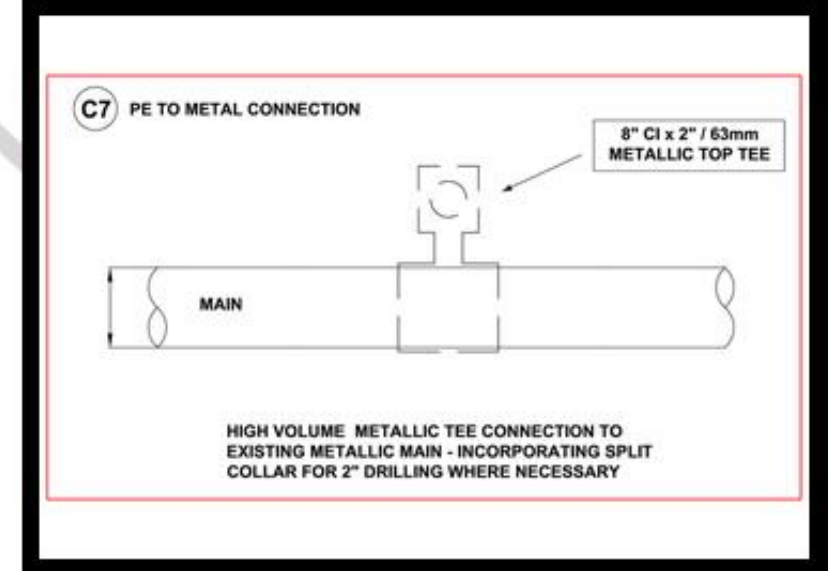
C7
MAIN
8" CI x 2" / 63mm METALLIC TOP TEE

PE TO METAL CONNECTION

HIGH VOLUME METALLIC TEE CONNECTION TO EXISTING METALLIC MAIN - INCORPORATING SPLIT COLLAR FOR 2" DRILLING WHERE NECESSARY

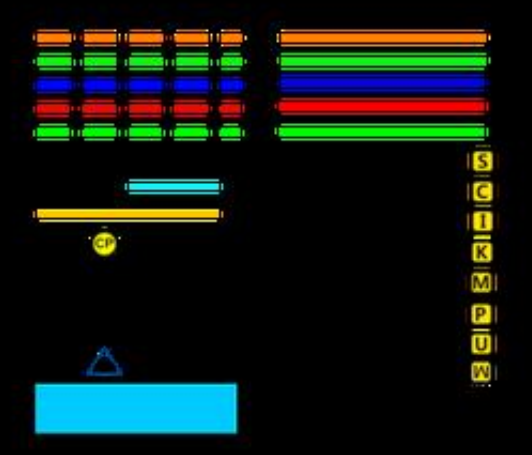
CP
S
C
I
K
M
P
U
W

LUKAS FRENAK 23-12-2021

Approved

1-0