



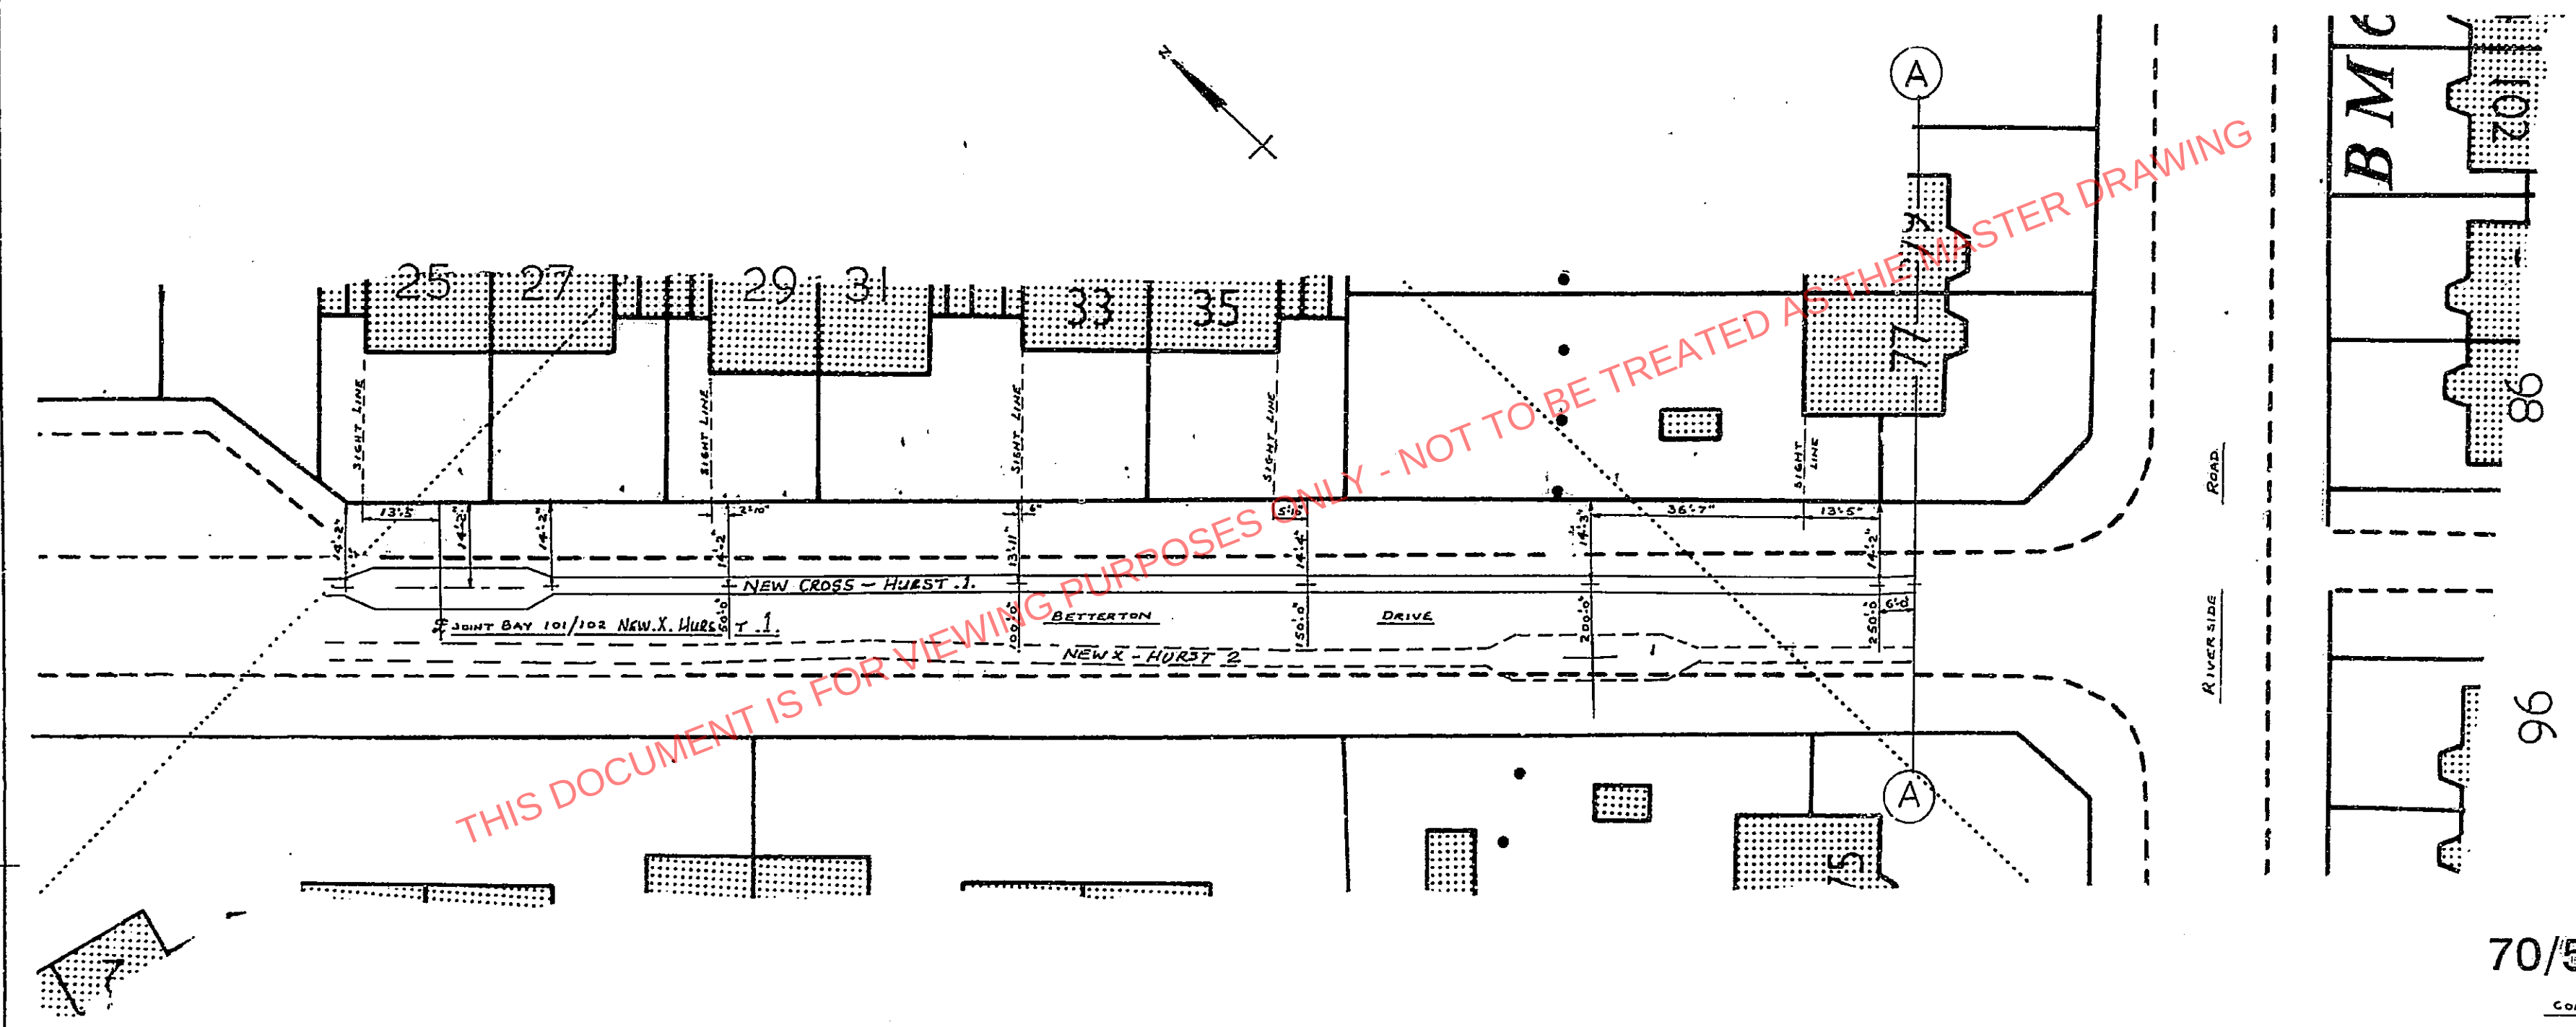

REPRODUCED FROM THE ORDNANCE SURVEY
MAP, WITH THE PERMISSION OF THE
CONTROLLER OF STATIONERY OFFICE.
CROWN COPYRIGHT RESERVED.
HALL HARDING LTD
427 Sydenham Road
Croydon

70/5691 SHT771

CONTINUED ON PAGE No. 565

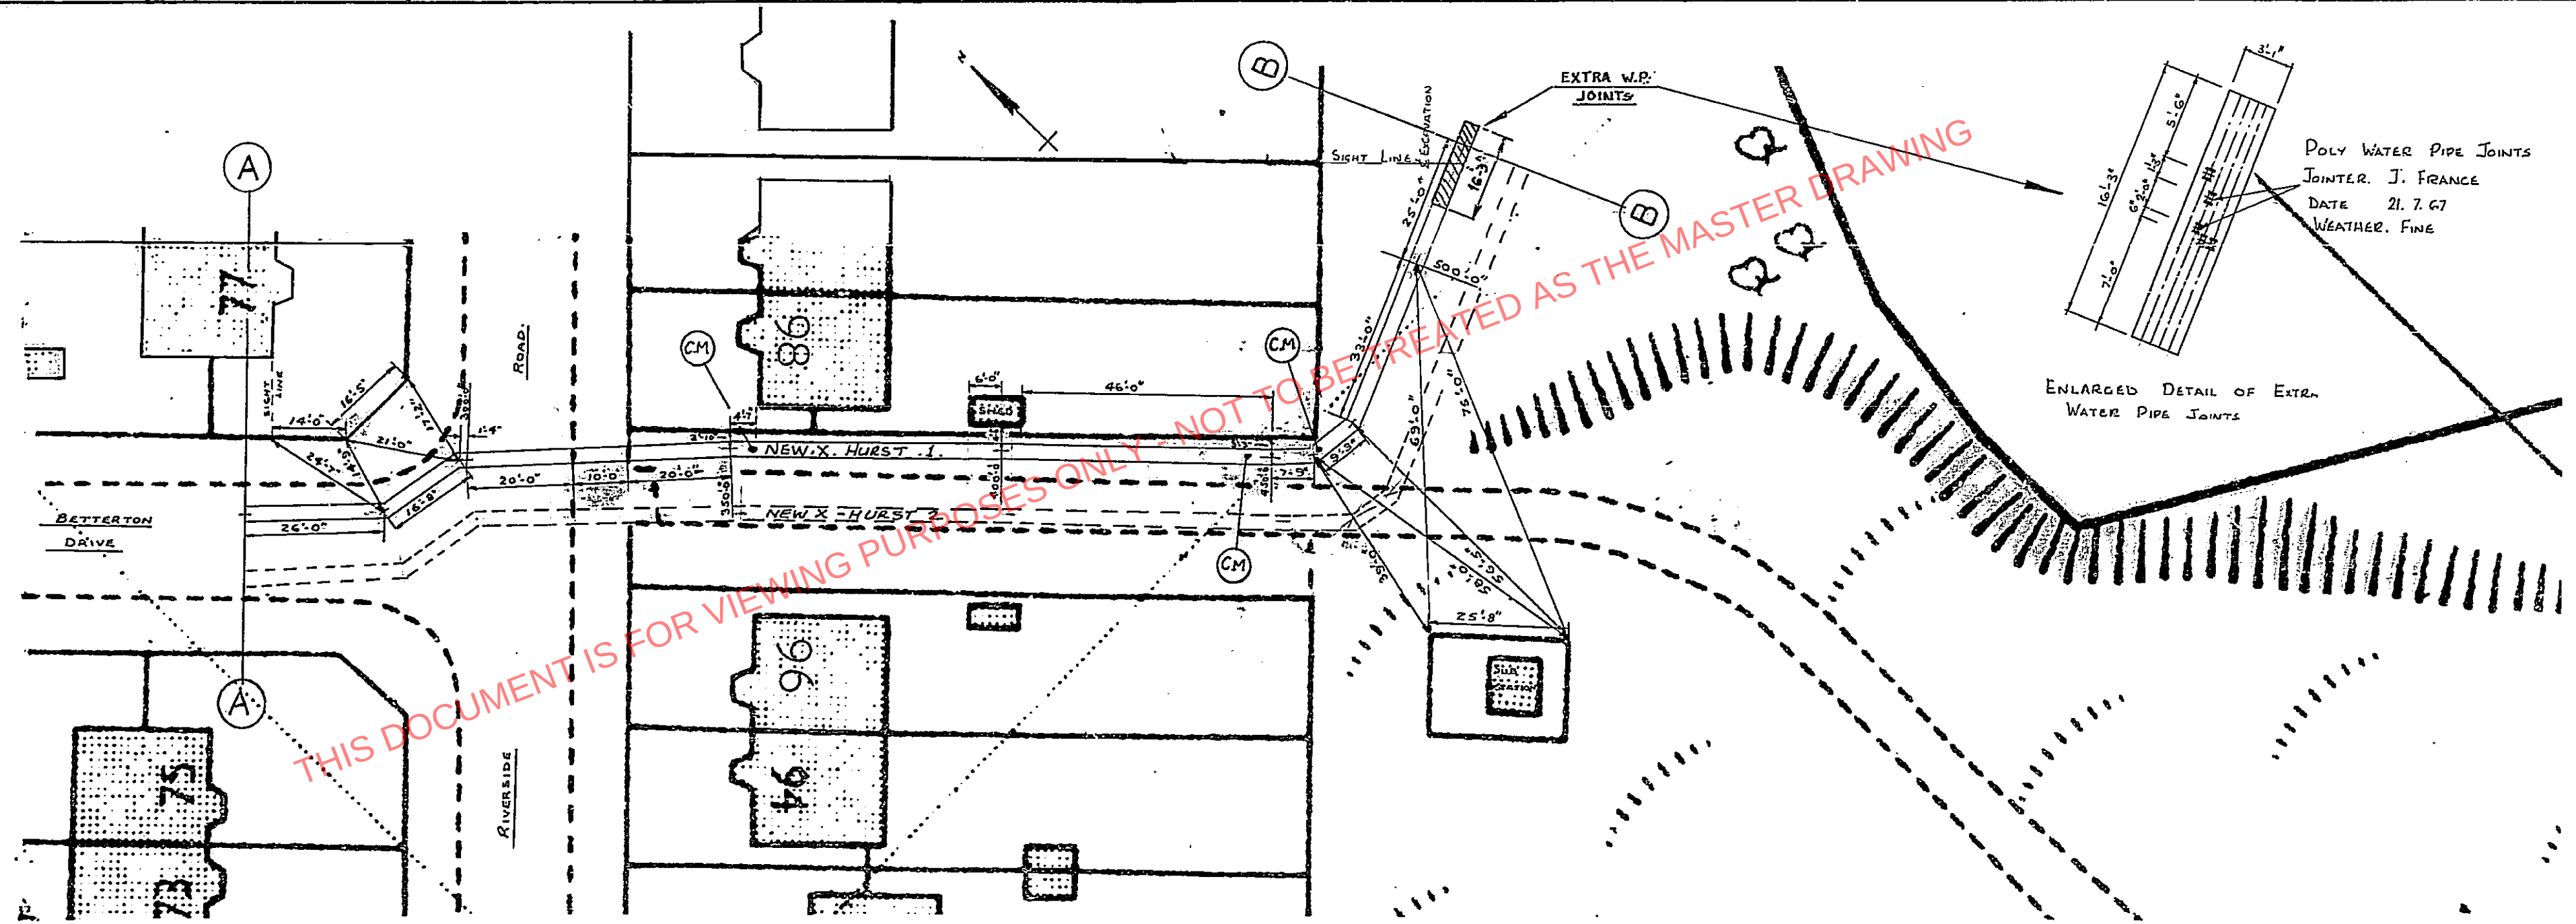

THIS DOCUMENT IS FOR VIEWING PURPOSES ONLY - NOT TO BE TREATED AS THE MASTER DRAWING

BETTERTON DRIVE

Dimensions from left to right:

- 50'-0"
- 50'-0"
- 50'-0"
- 50'-0"

ROAD LEVEL

275 KV CABLE SLABS

No. 77


TOP OF SLABS


150'-0" AT 9 1/2" CRS.

THIS DOCUMENT IS FOR VIEWING PURPOSES ONLY


DEPTHS TO BOTTOM OF TRENCH ARE SHOWN IN CIRCLES

70/5691 SHT774

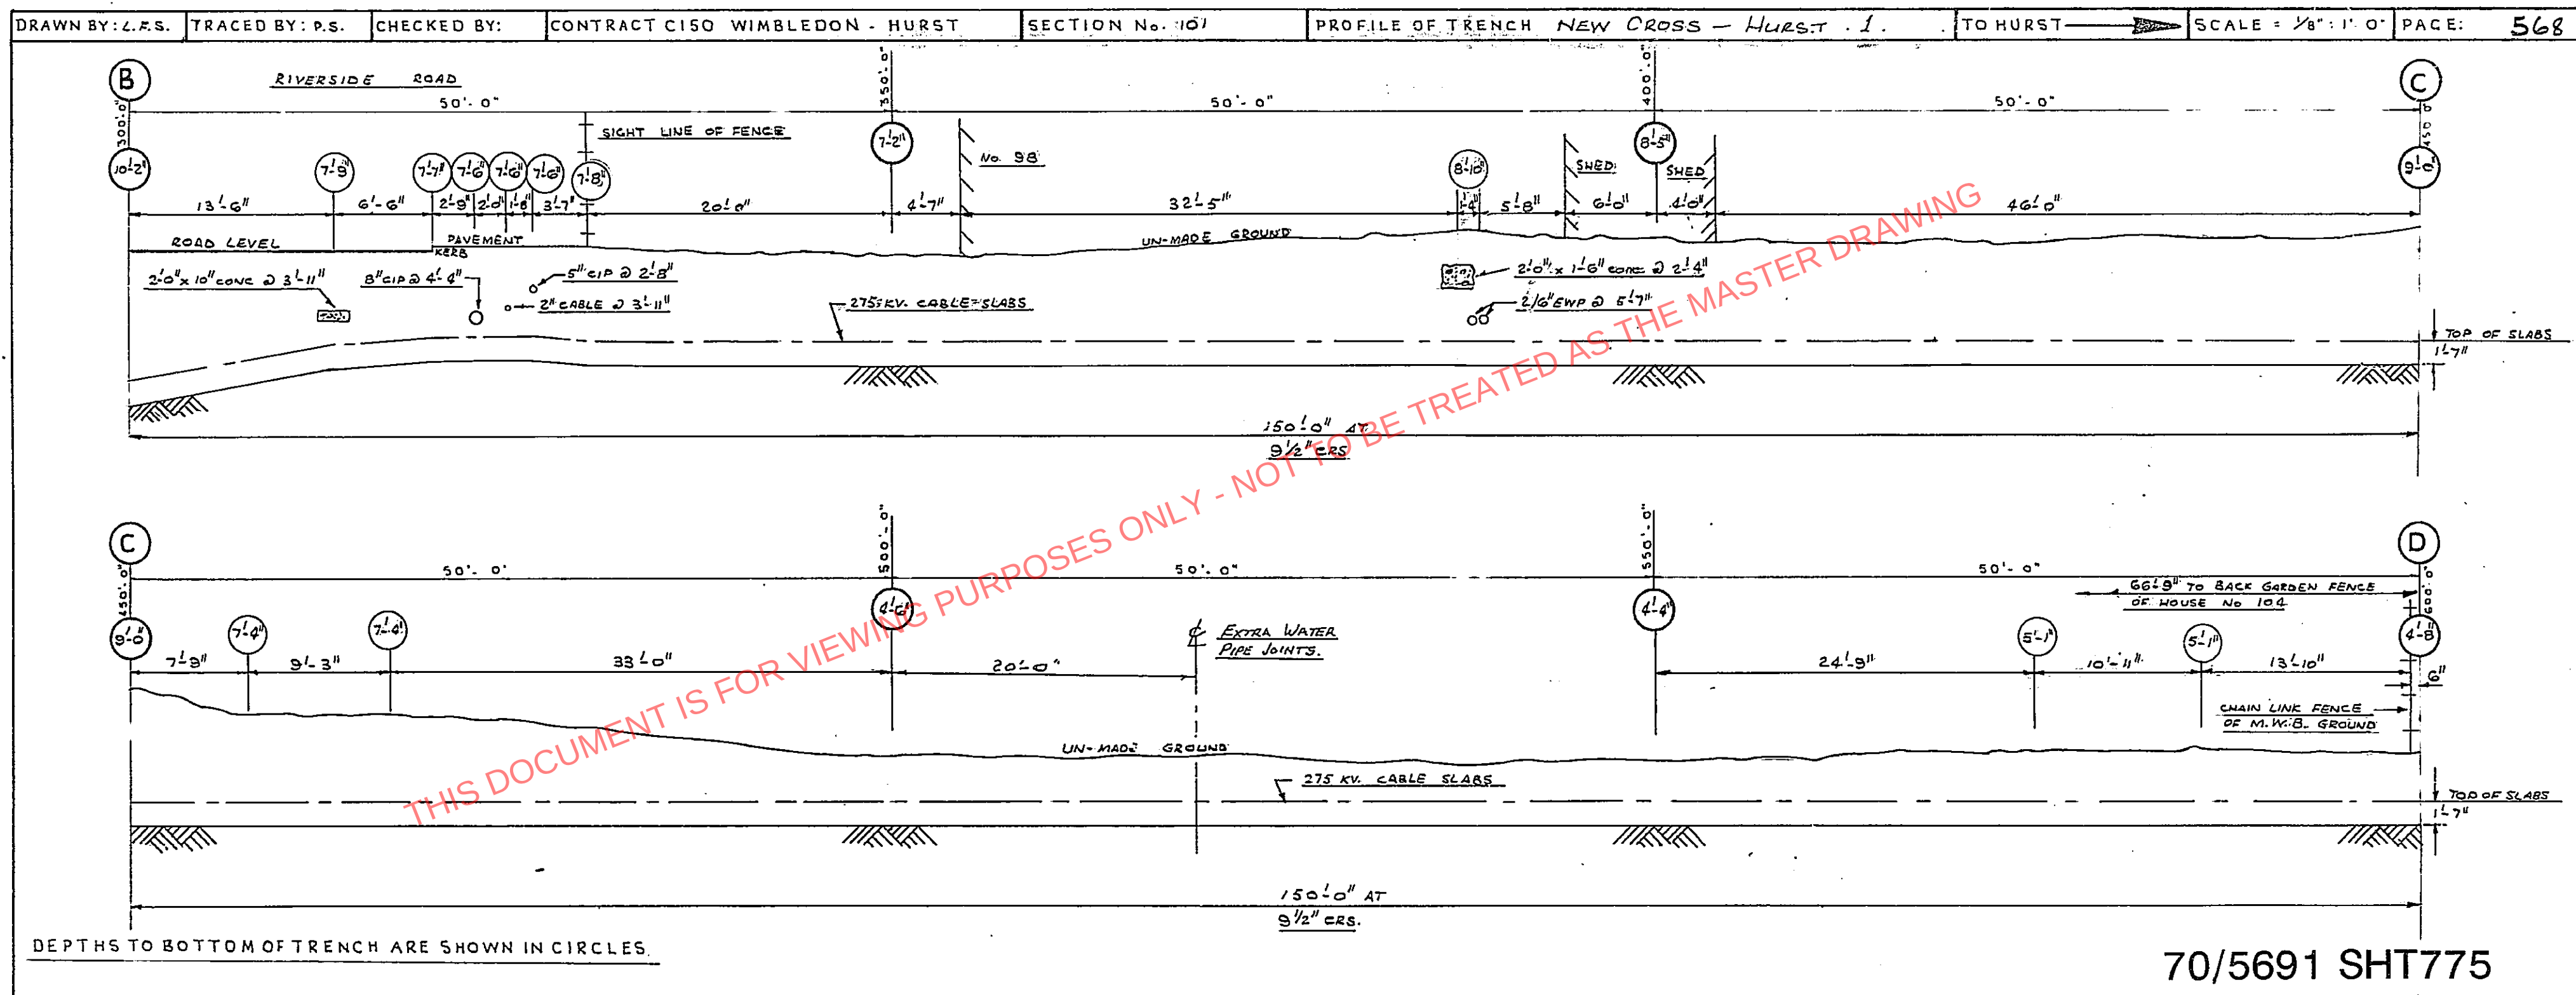


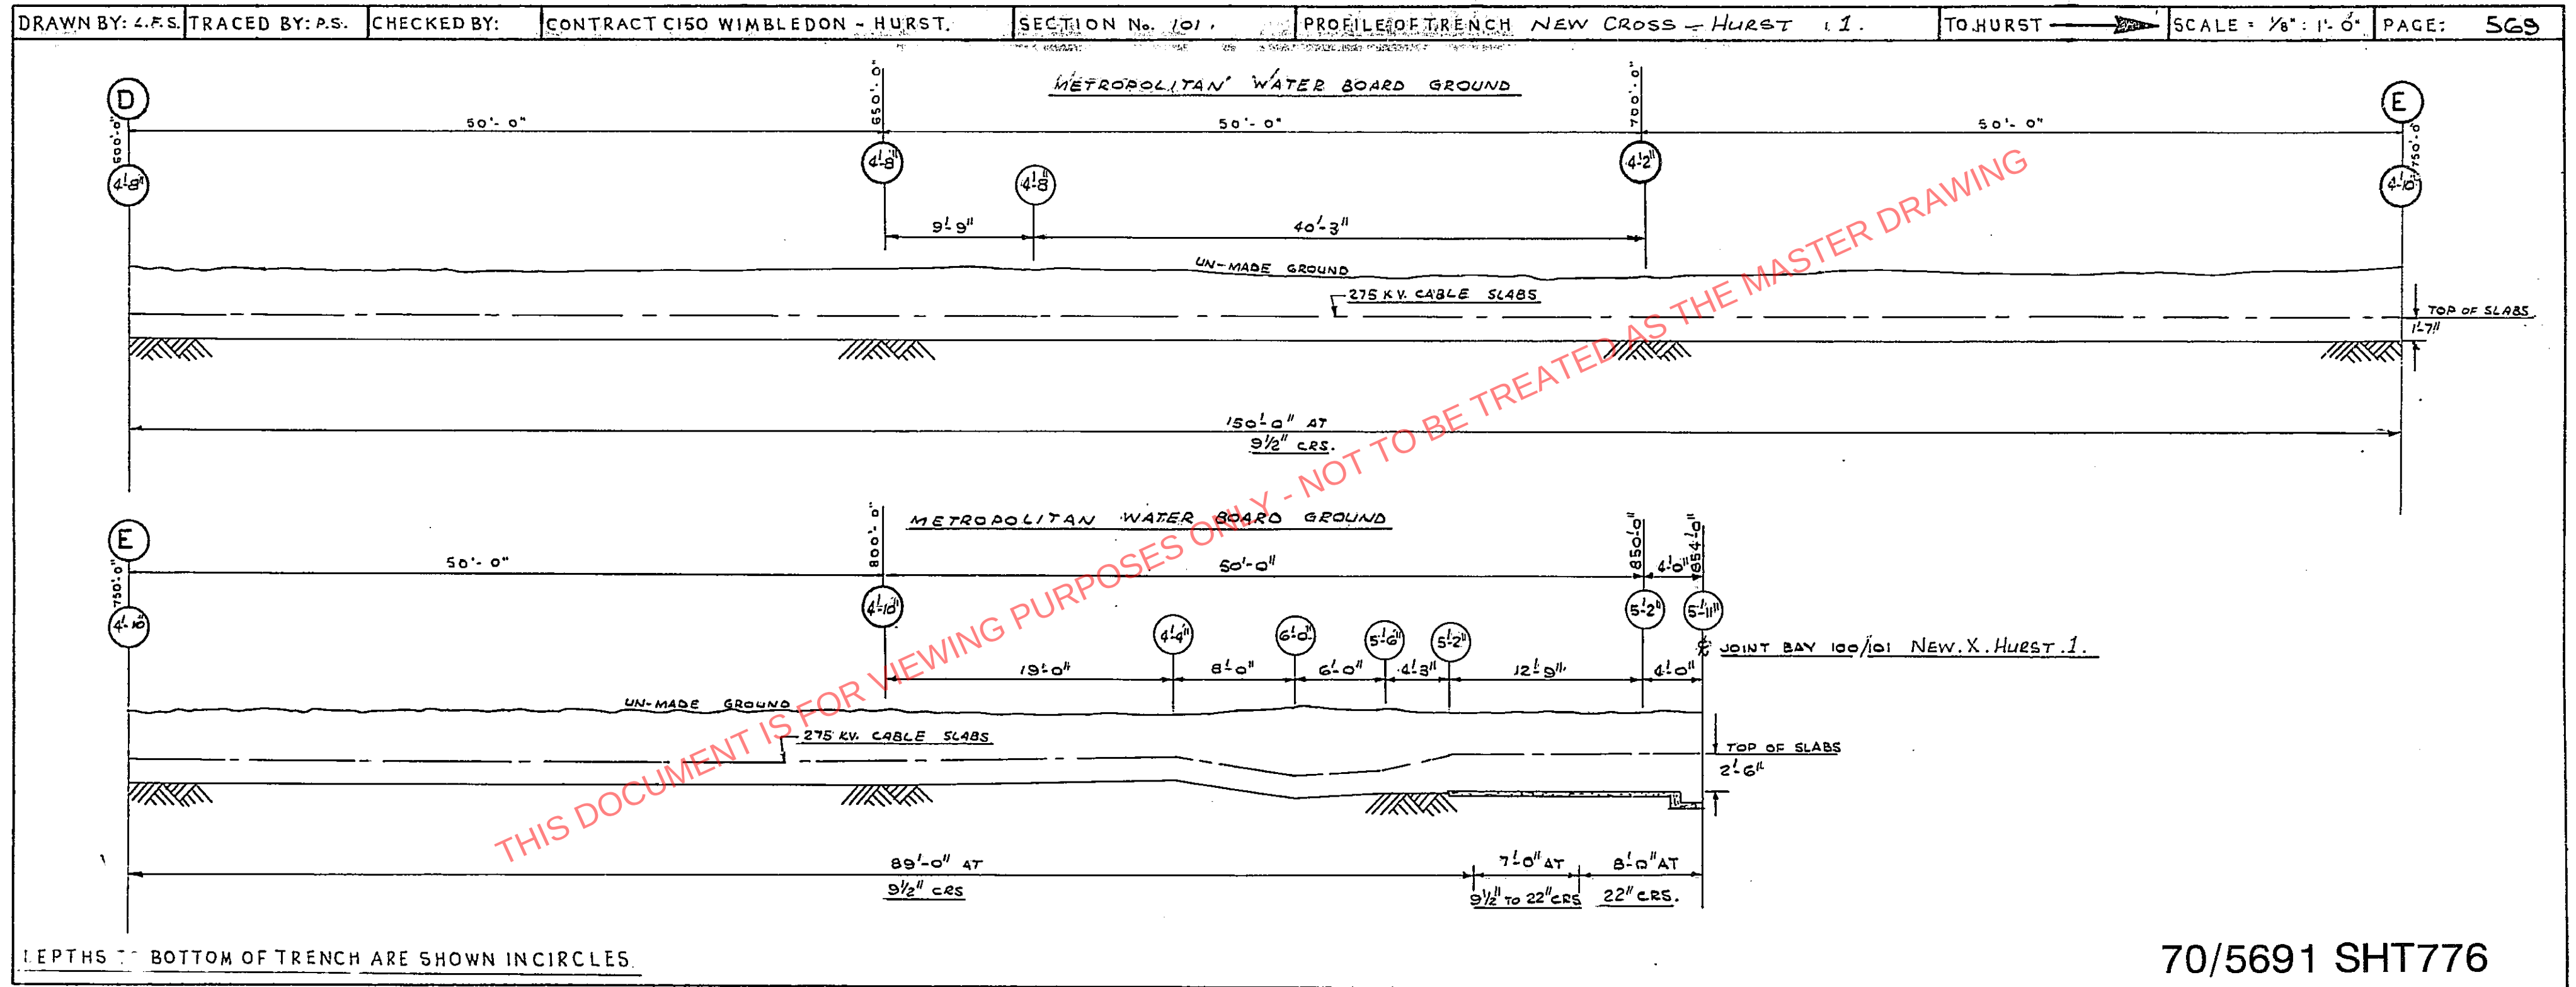


TYPICAL TRENCH SECTIONS.

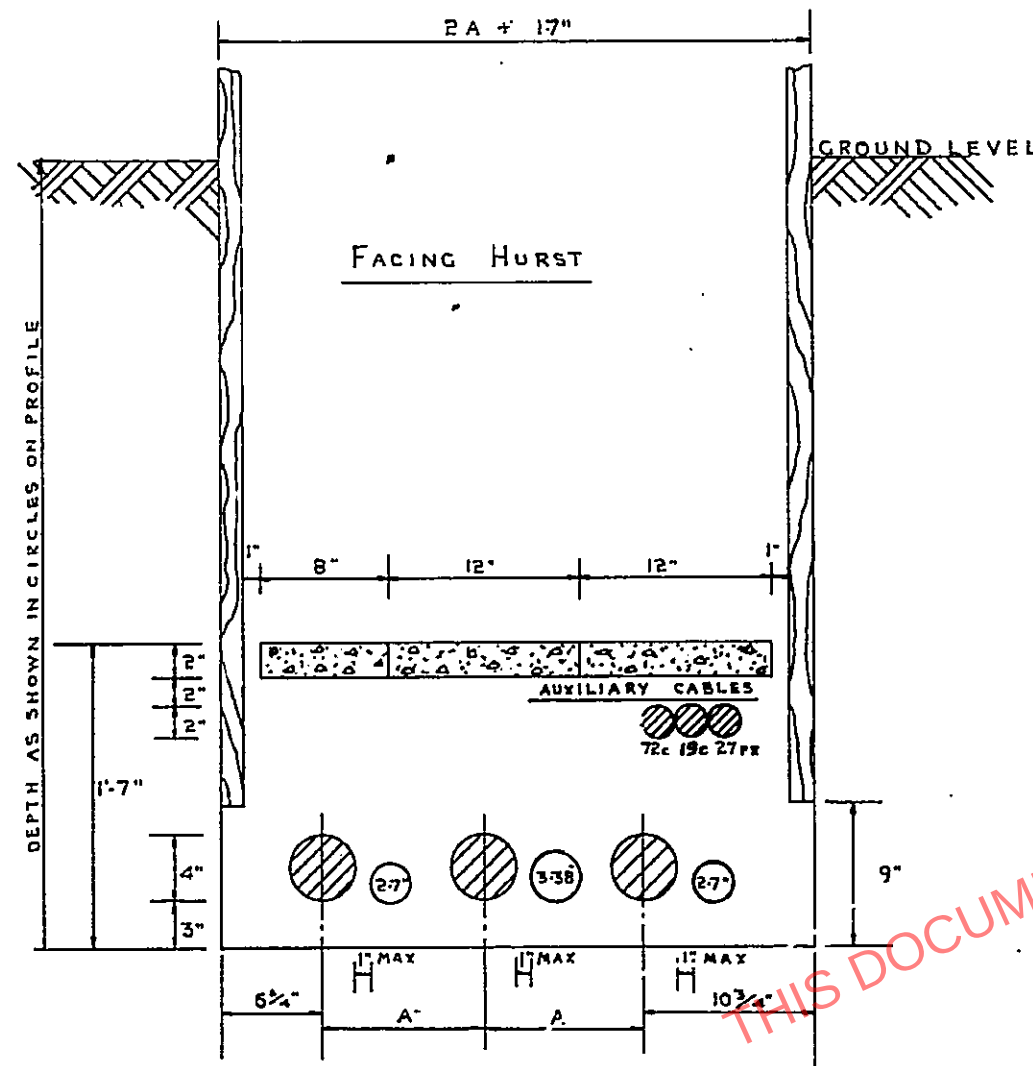

**C.S.A. ODD NUMBER
CABLE SECTION.**

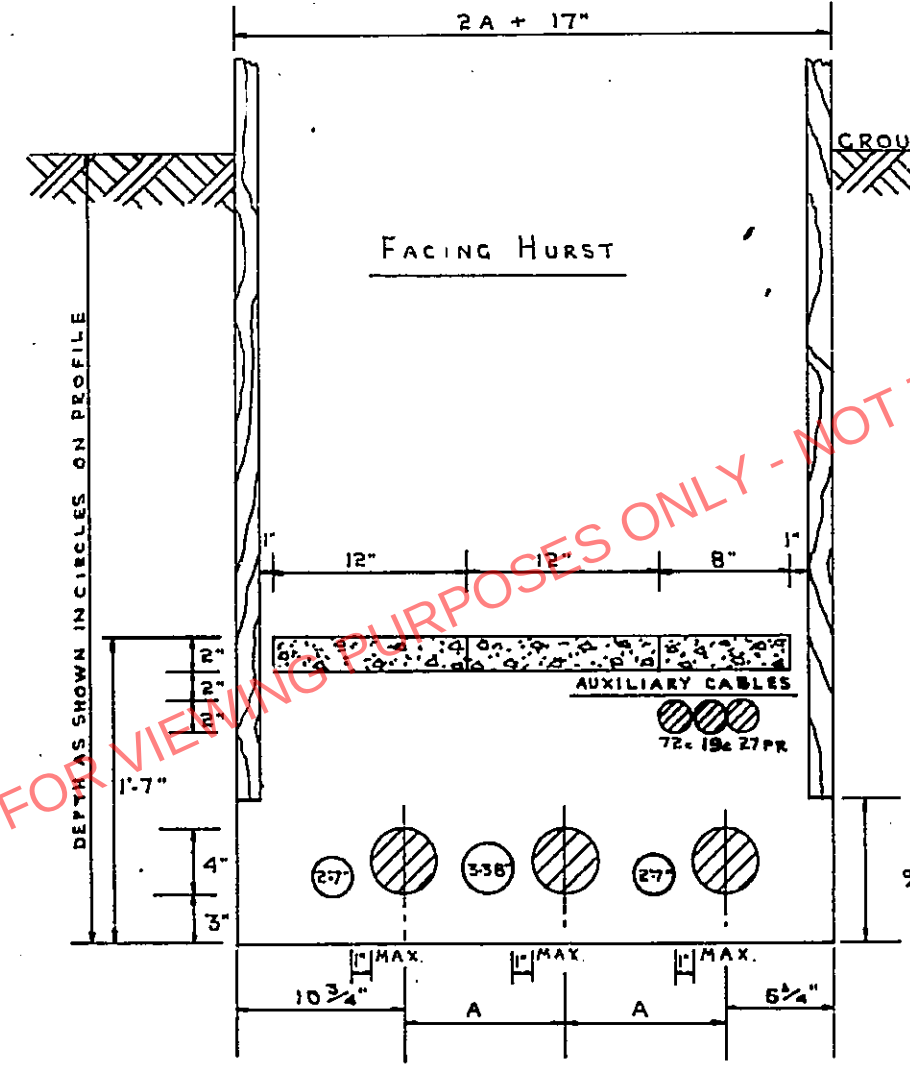

**C.S.A. EVEN NUMBER
CABLE SECTION.**

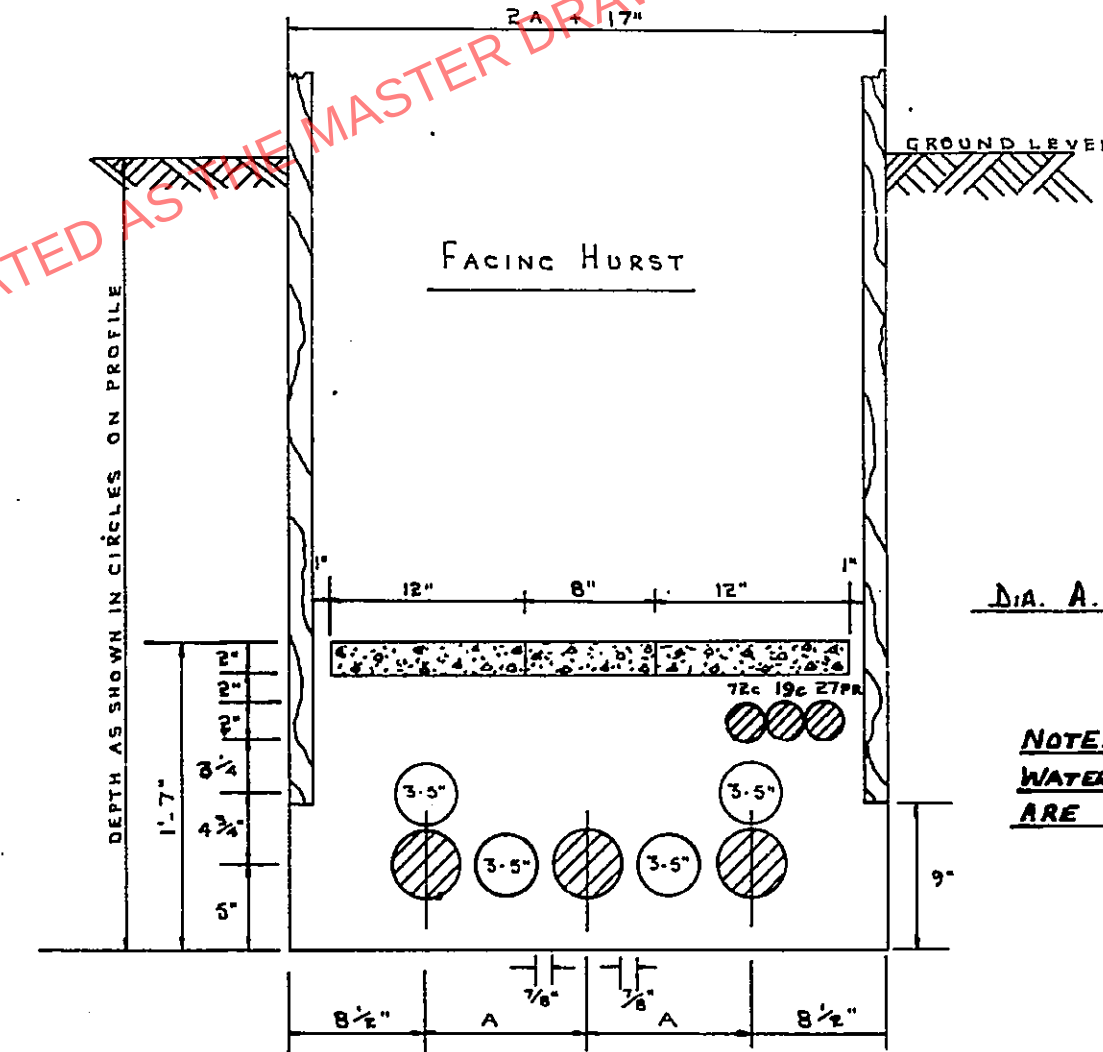

**POLYTHENE ODD AND EVEN
NUMBER CABLE SECTION.**

DIA. A. AS SHOWN ON SECTION
PROFILES

NOTE:
WATER PIPE DIAMETERS
ARE OVERALL

70/5691 SHT136