




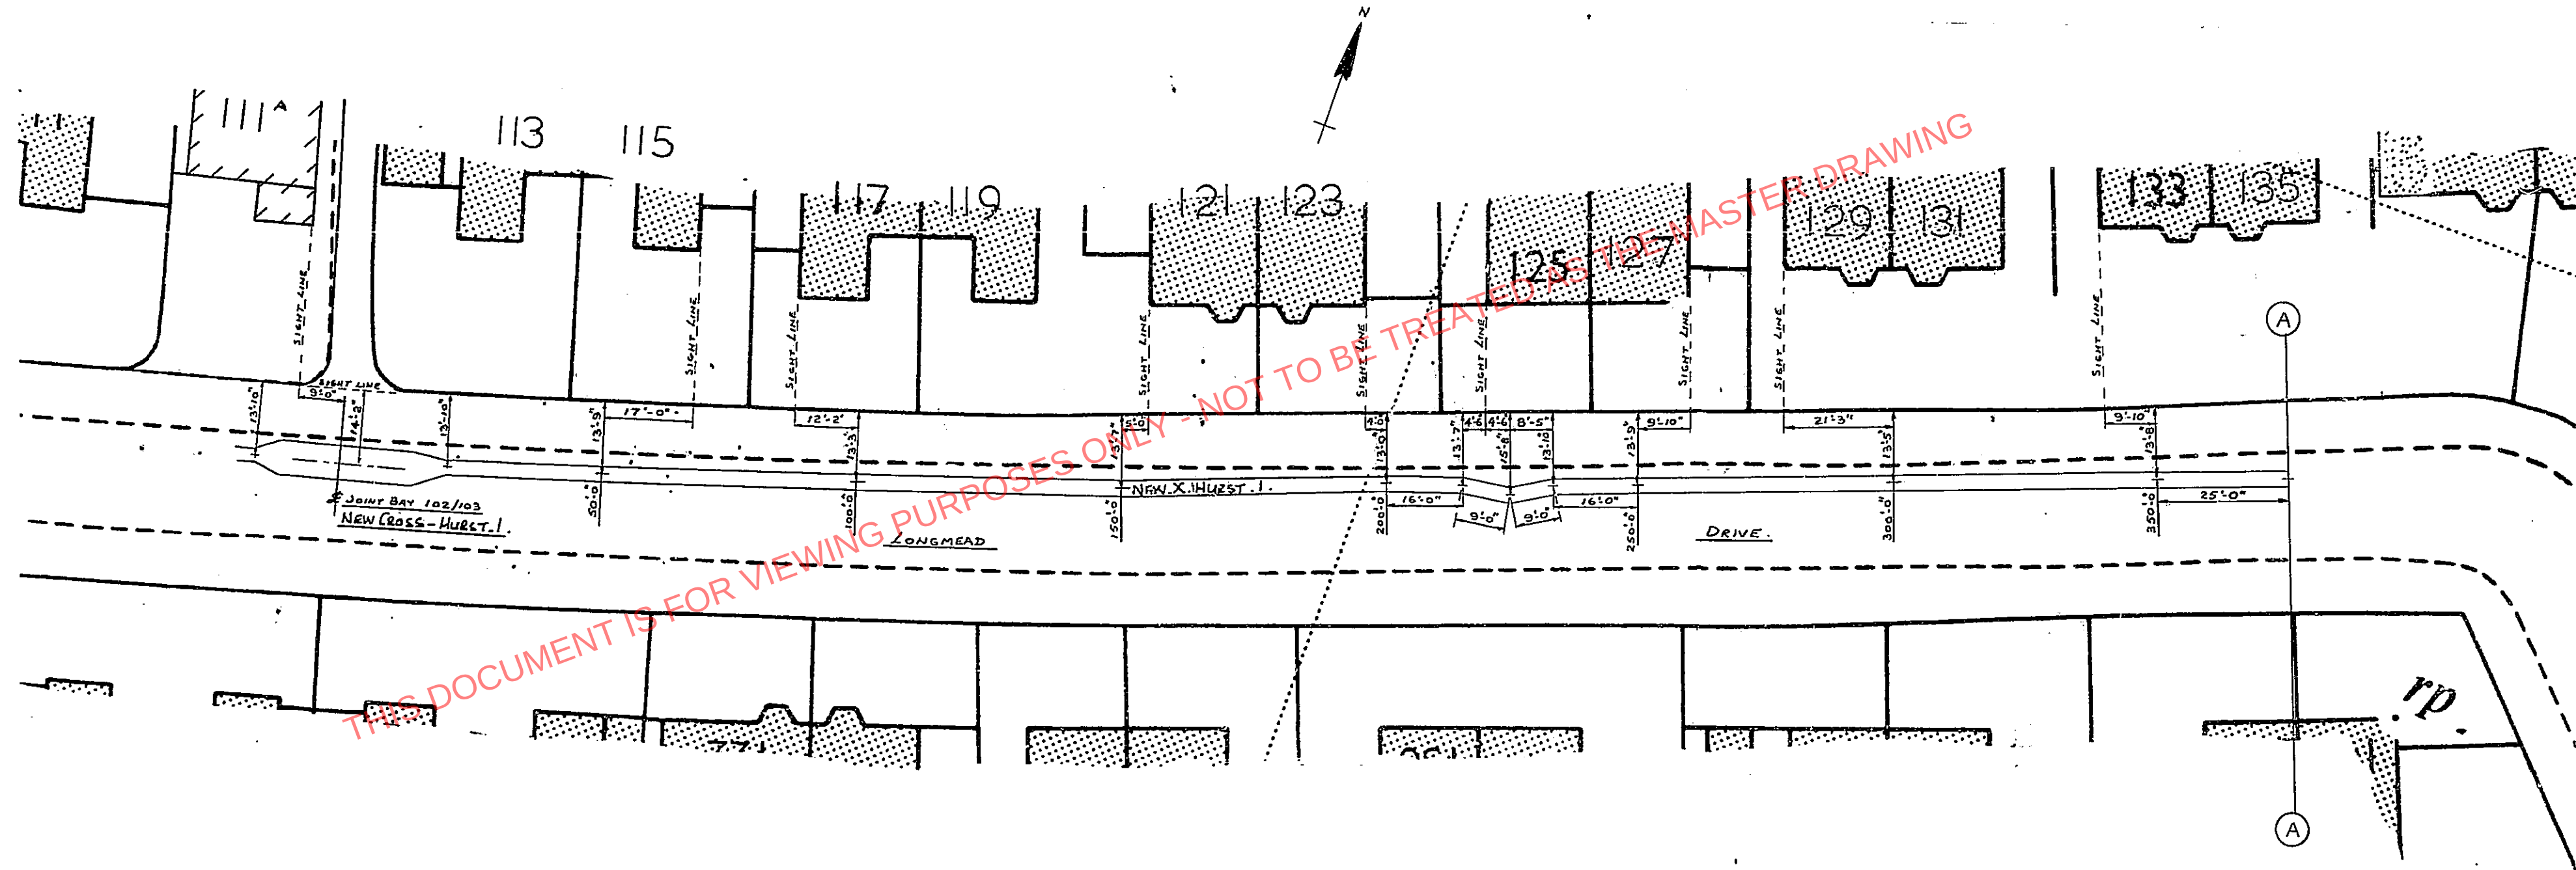


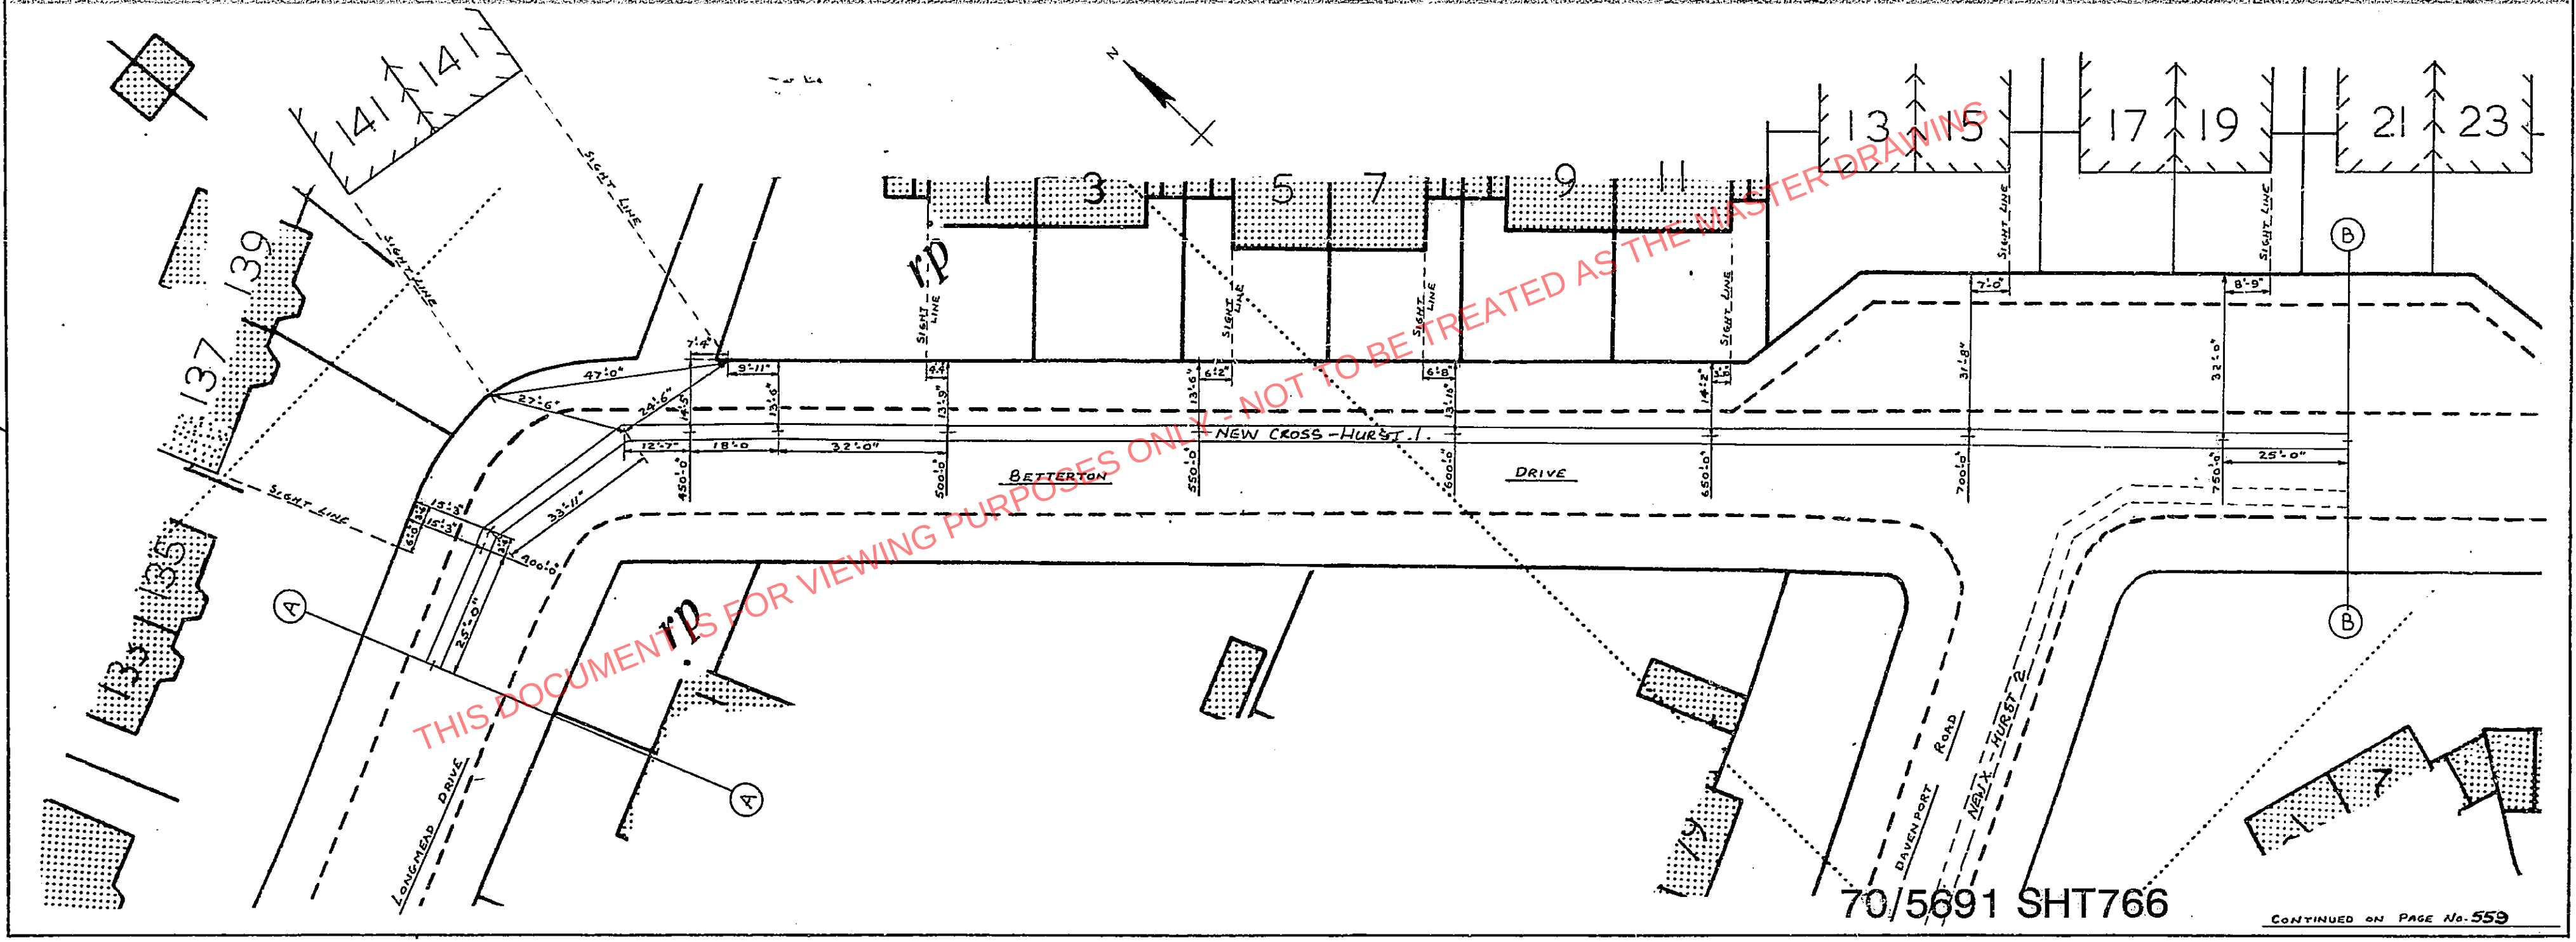



REPRODUCED FROM THE ORDNANCE SURVEY
MAP, WITH THE PERMISSION OF THE
CONTROLLER OF THE STATIONERY OFFICE.
CROWN COPYRIGHT RESERVED.
HALL HARDING LTD
401 Sydenham Road Croydon

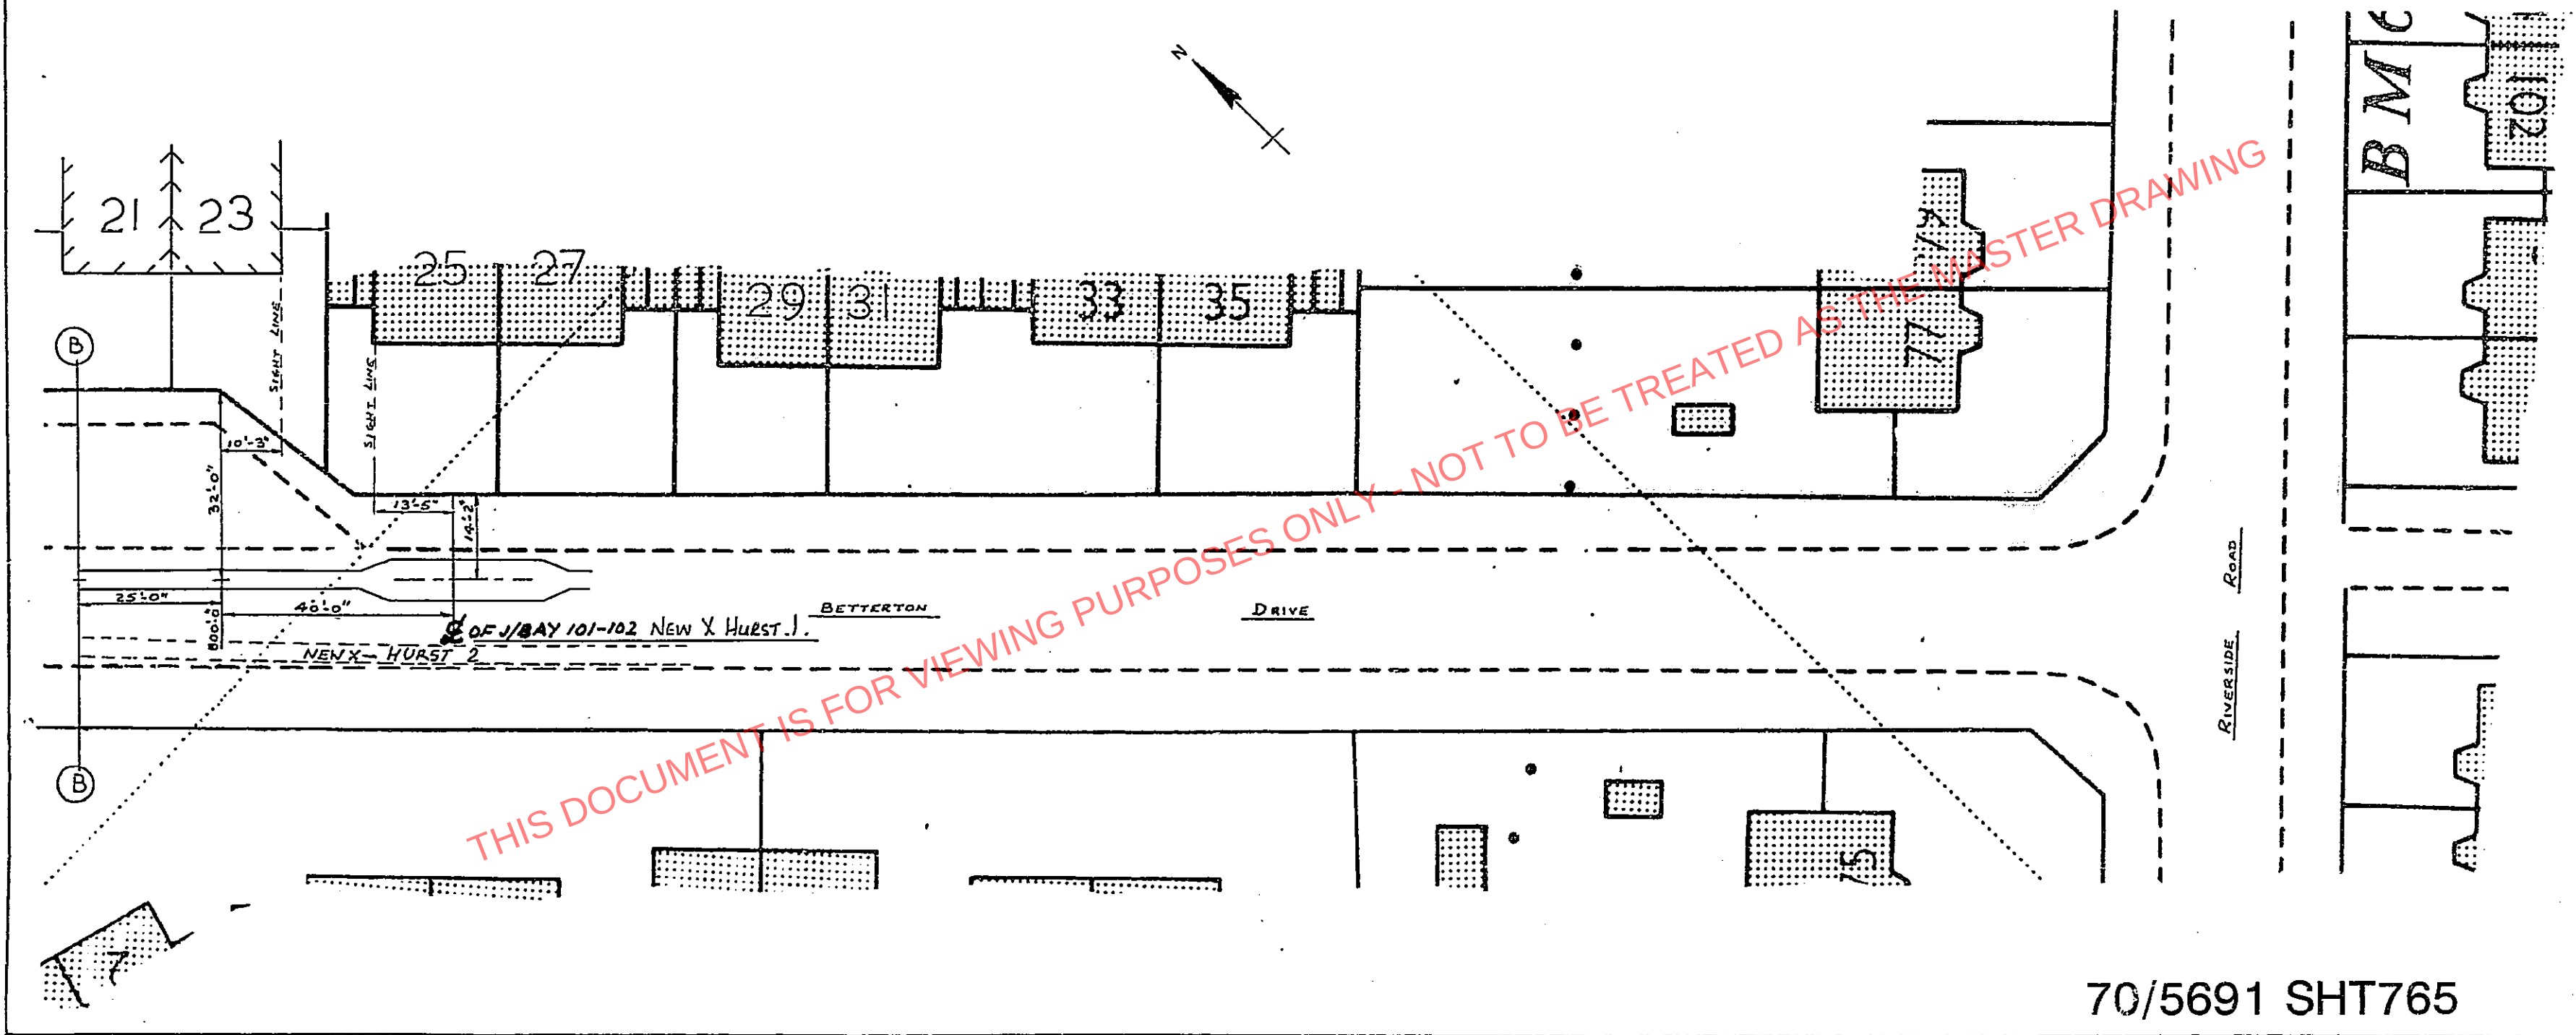

REPRODUCED FROM THE ORDNANCE SURVEY
MAP WITH THE ACTION OF THE
CONTROLLER OF STATIONERY OFFICE
CROWN COPYRIGHT RESERVED
HALL HARDING LTD
423 Sydenham Road
Croydon

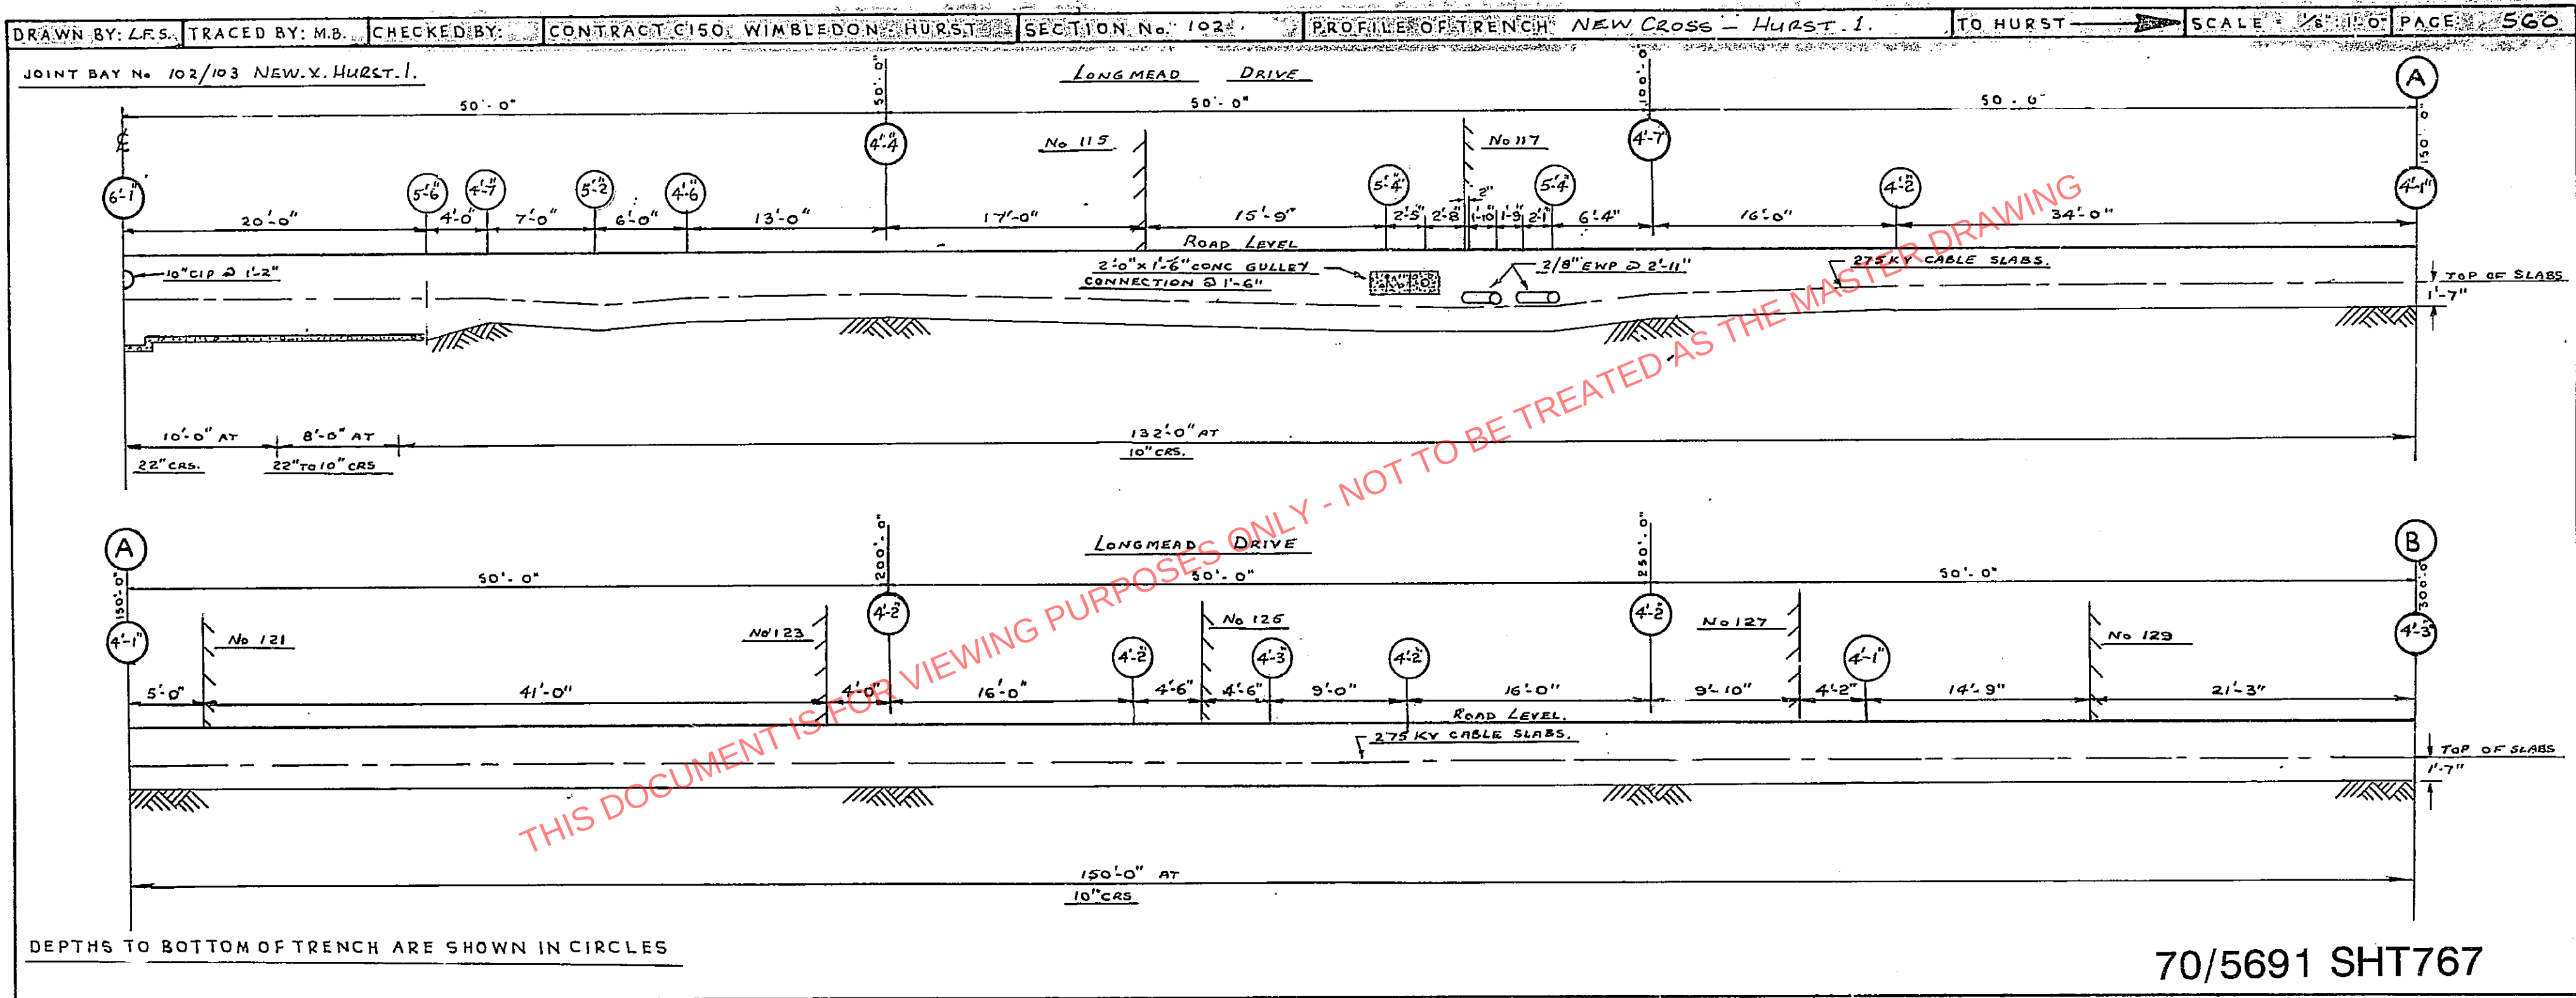

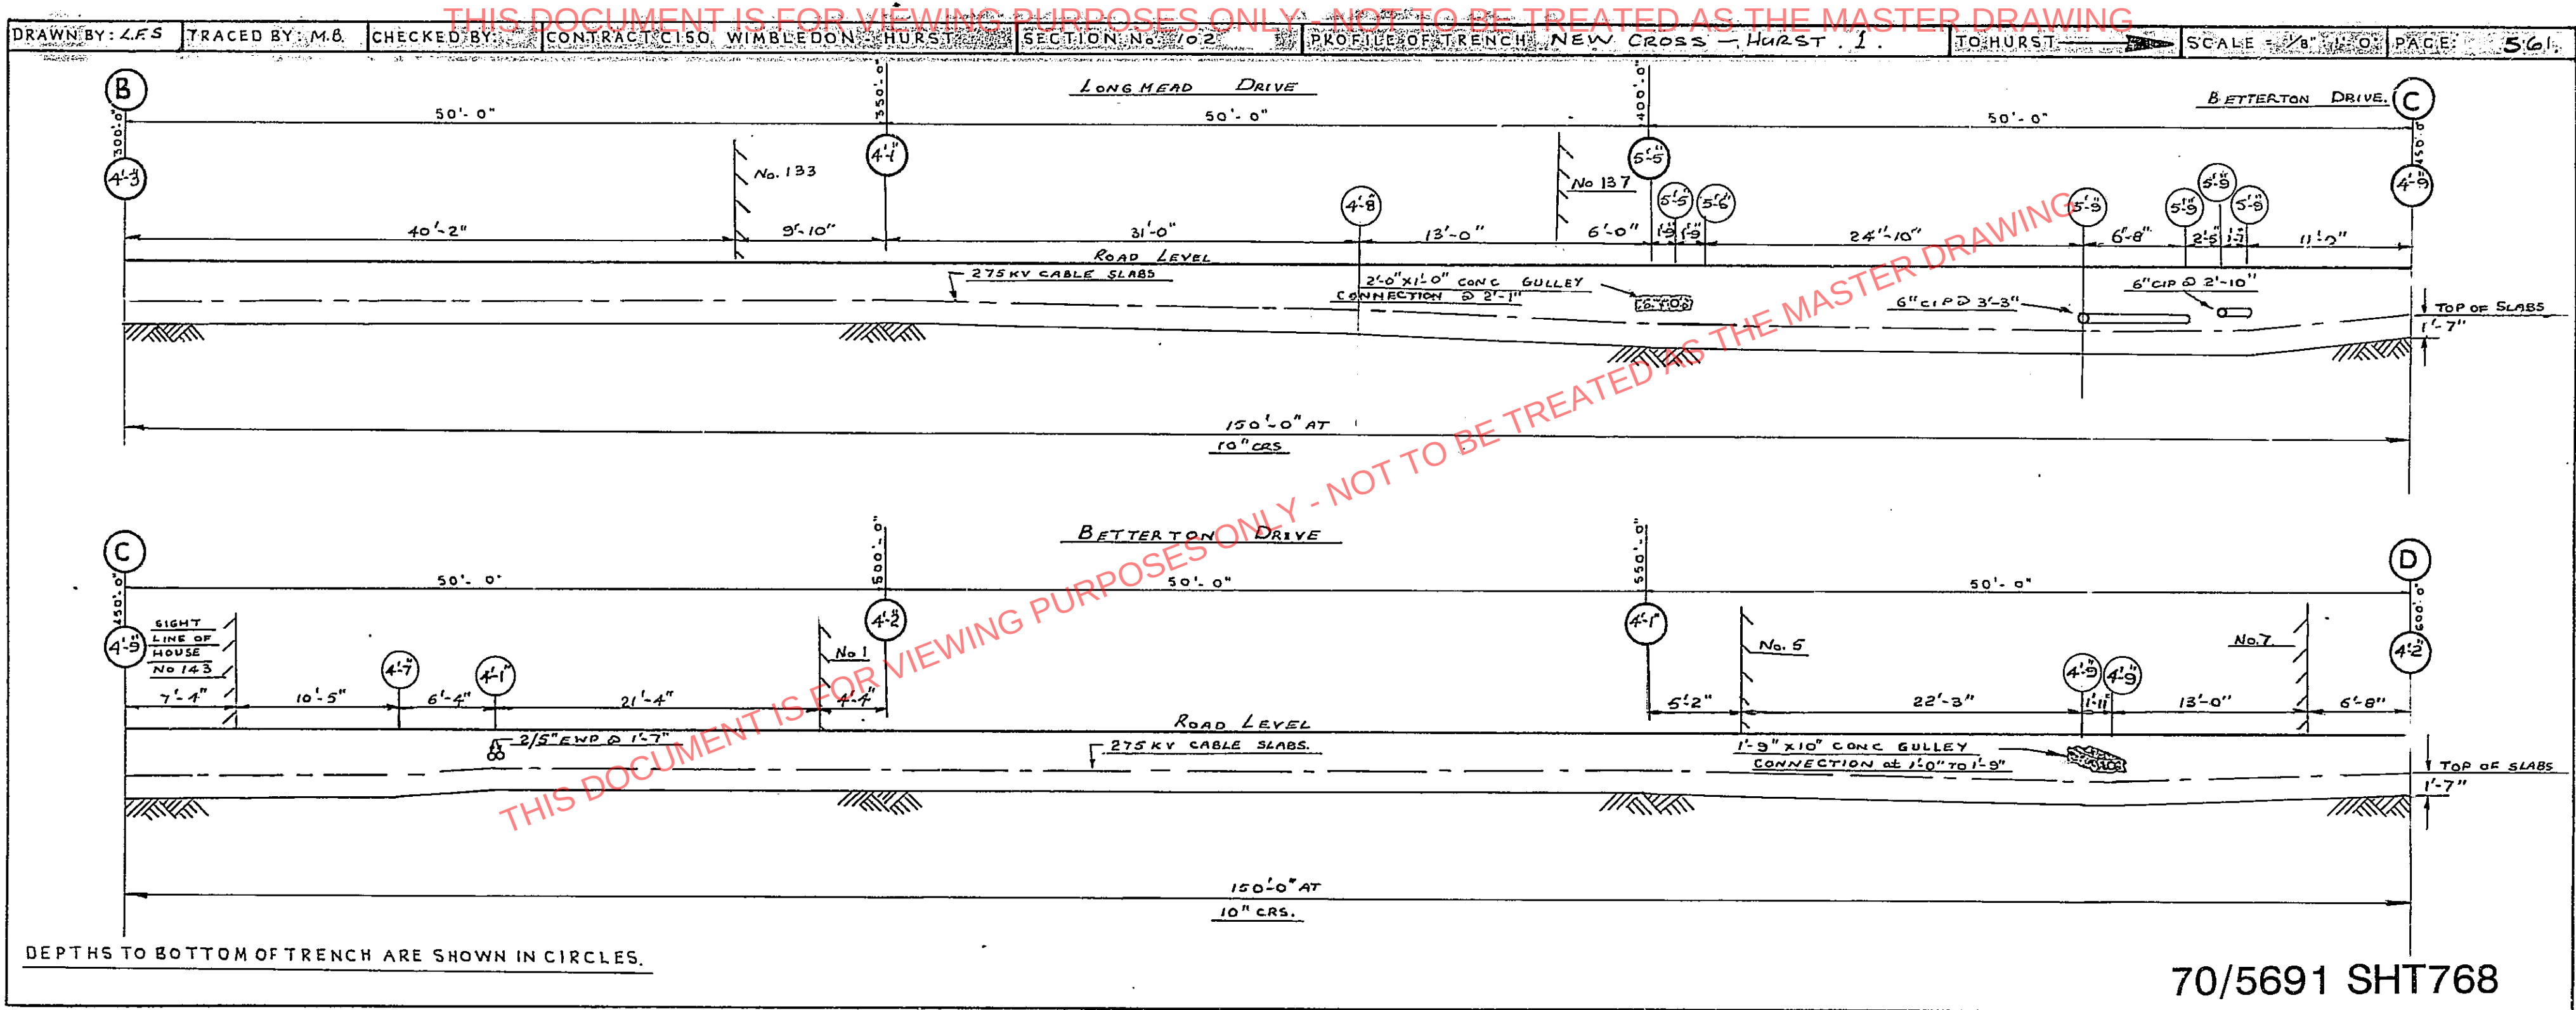


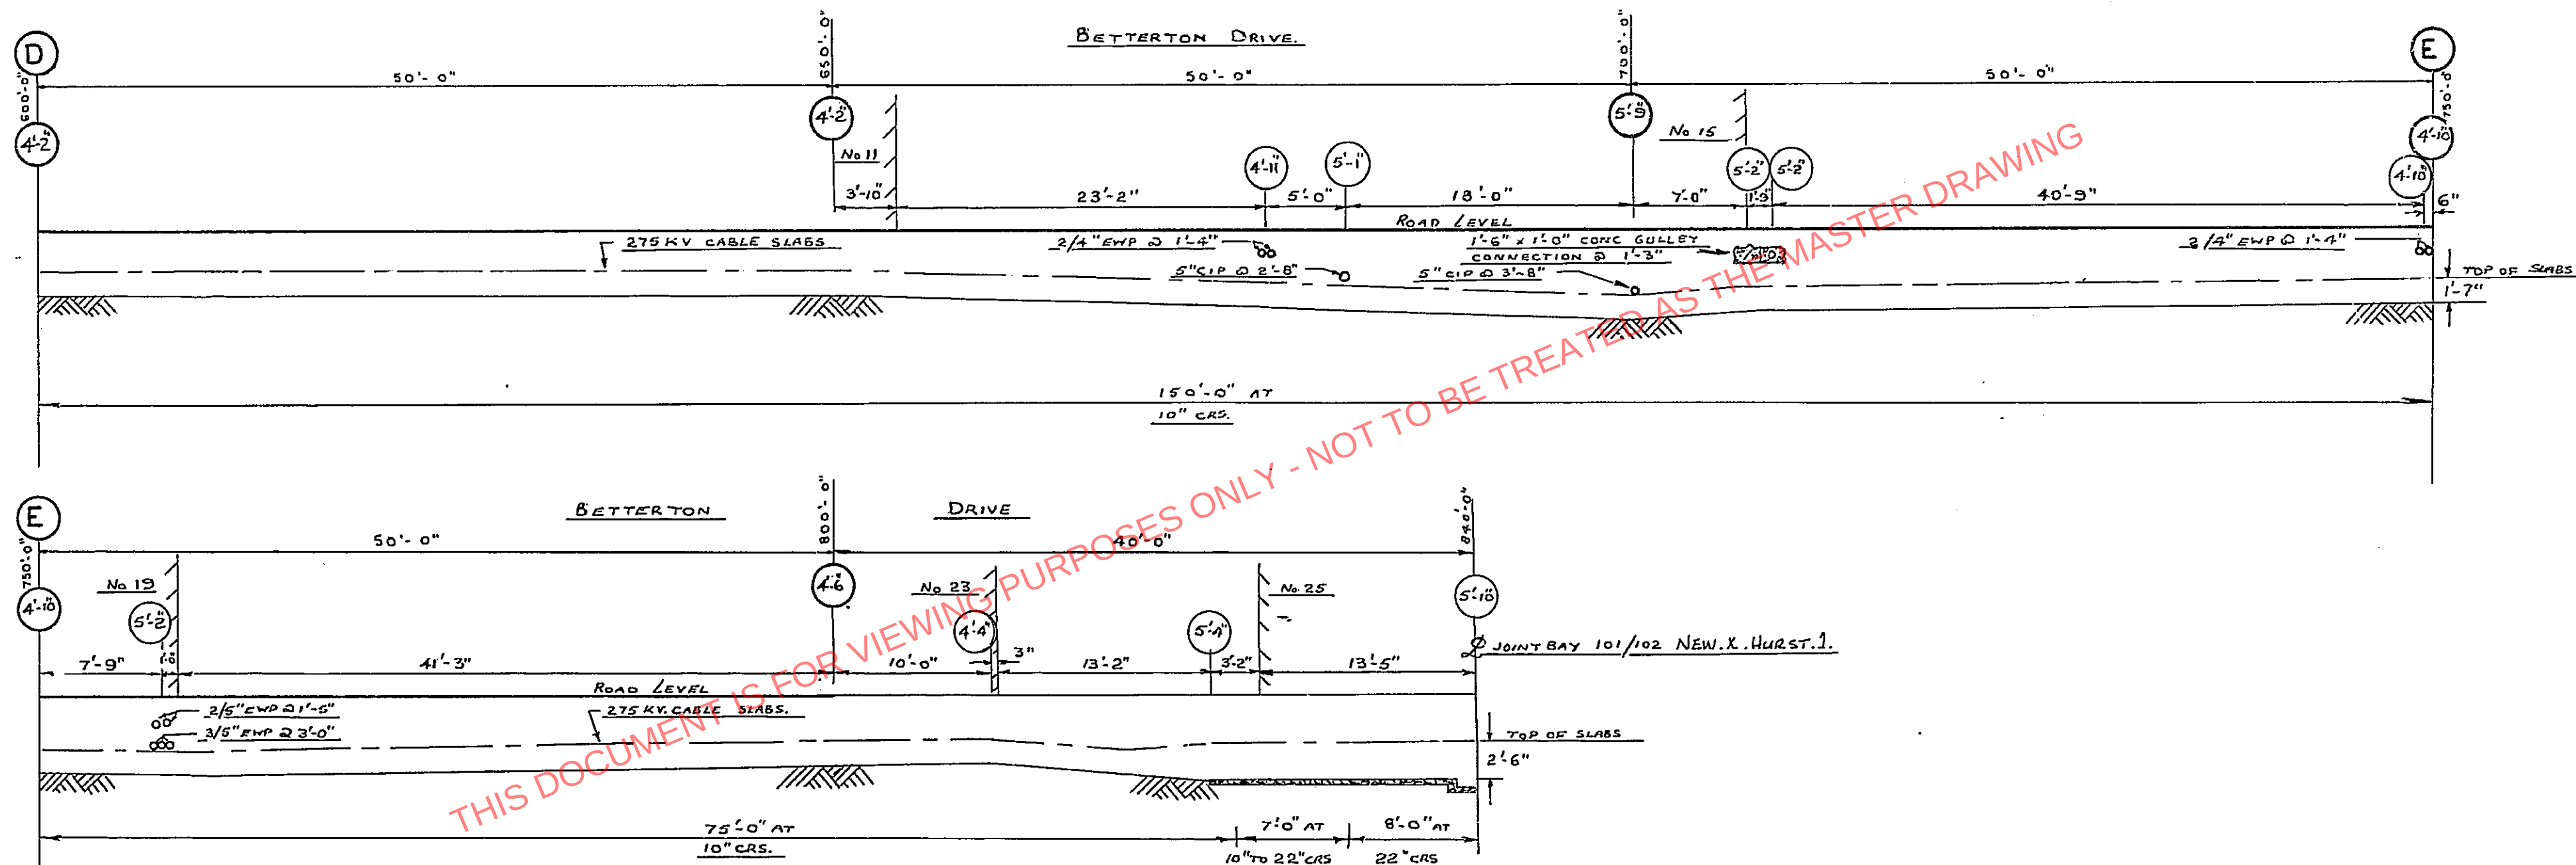


DEPTHS TO BOTTOM OF TRENCH ARE SHOWN IN CIRCLES.

70/5691 SHT769


TYPICAL TRENCH SECTIONS.

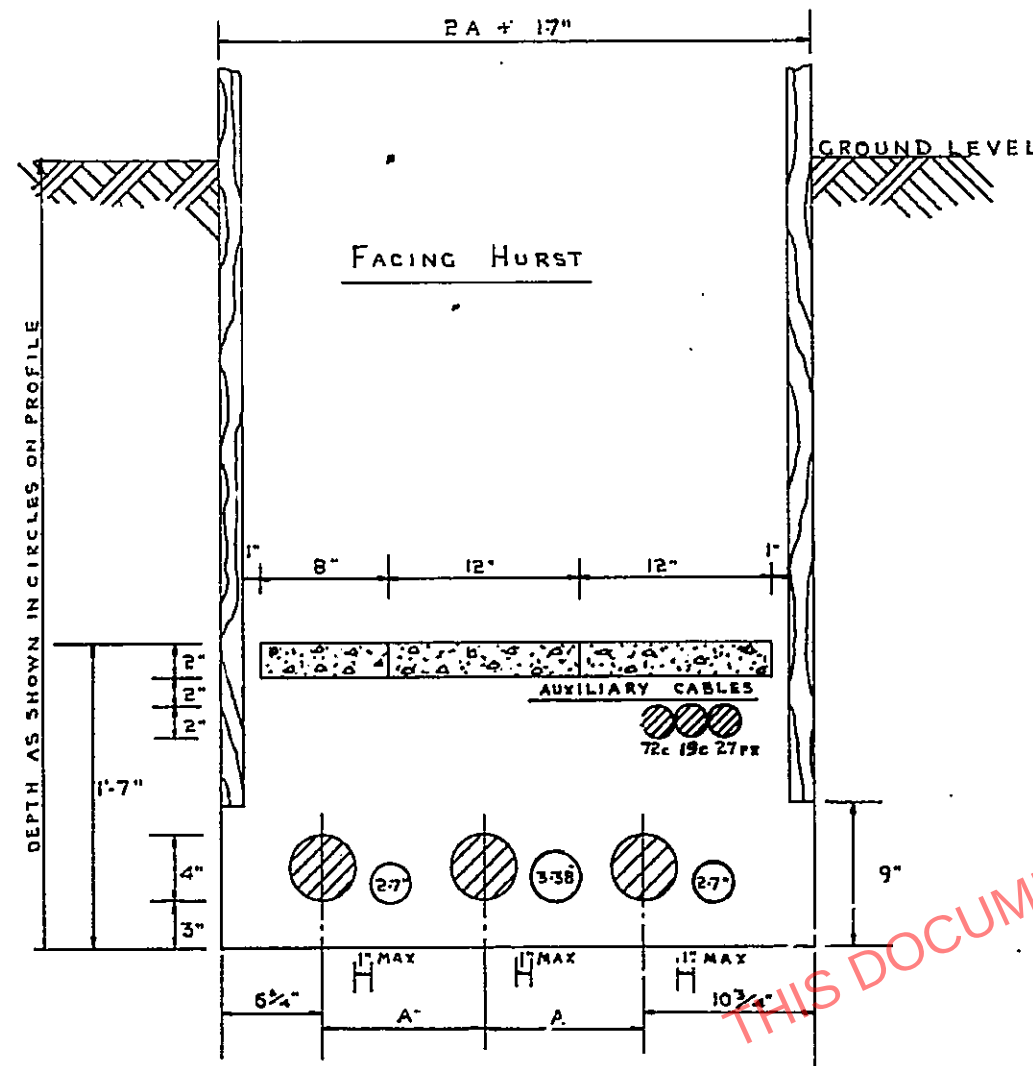

**C.S.A. ODD NUMBER
CABLE SECTION.**

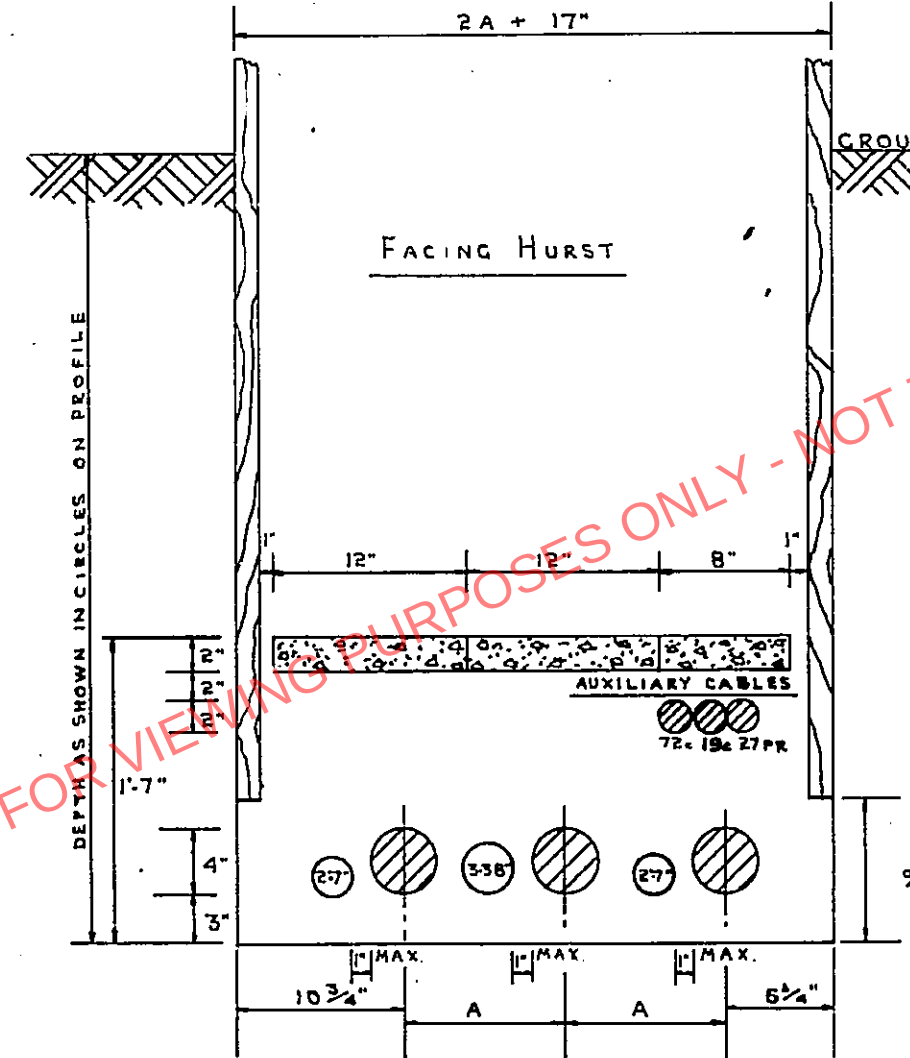

**C.S.A. EVEN NUMBER
CABLE SECTION.**

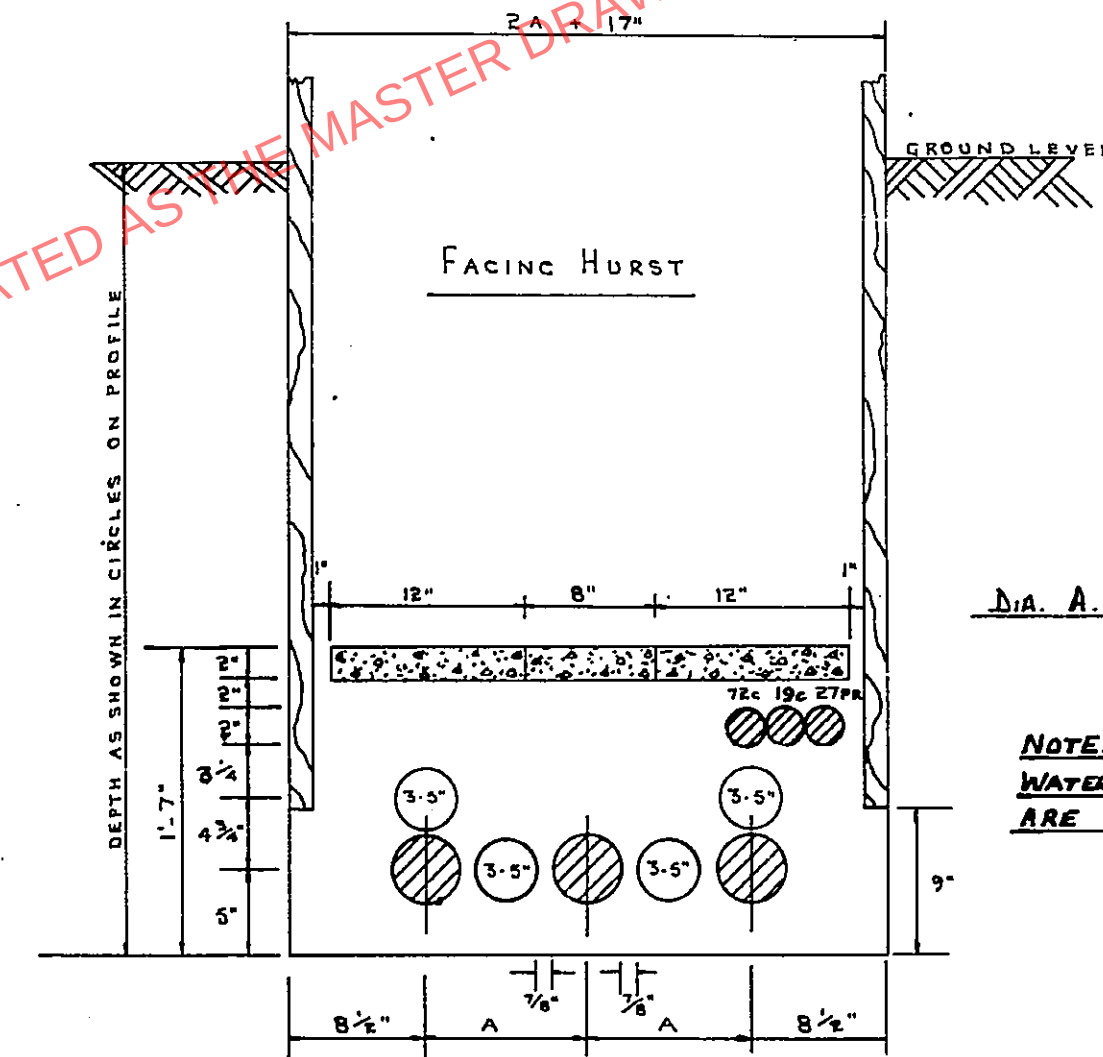

**POLYTHENE ODD AND EVEN
NUMBER CABLE SECTION.**

DIA. A. AS SHOWN ON SECTION
PROFILES

NOTE:
WATER PIPE DIAMETERS
ARE OVERALL

70/5691 SHT136